



ALL LOOSE FURNITURE &  
MATERIAL CODE TO CLIENT  
SELECTION

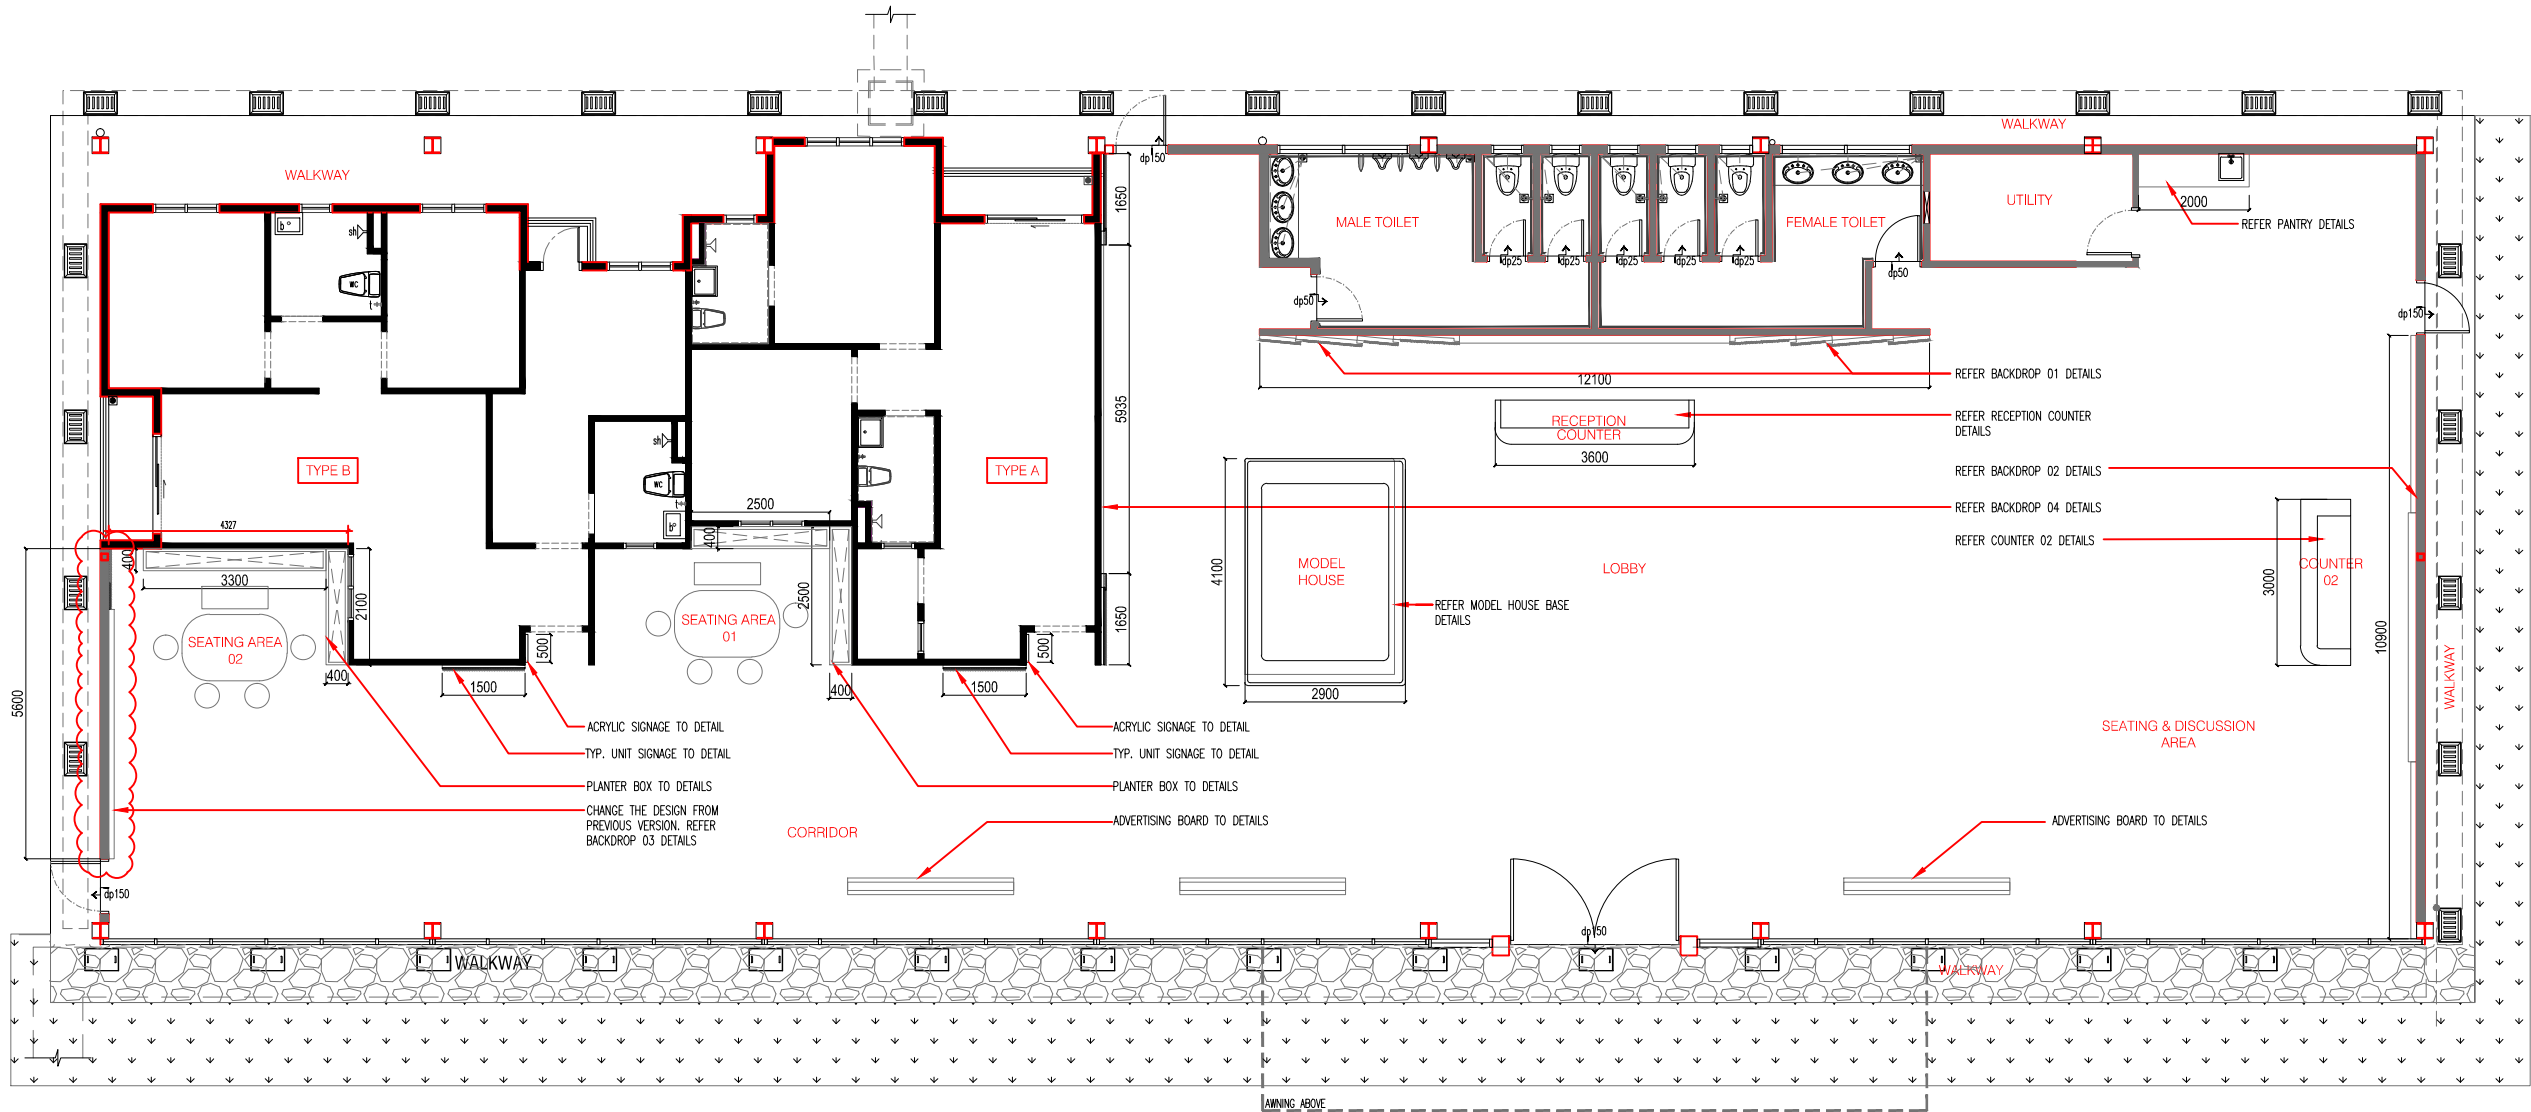


LOT 26662, BUKIT BARU SALES GALLERY  
MAIN LOBBY FLOOR PLAN


|  |   |                                                                                               |         |          |                                                                                |          |
|--|---|-----------------------------------------------------------------------------------------------|---------|----------|--------------------------------------------------------------------------------|----------|
|  | THIS DRAWING IS COPYRIGHTED. CONTRACTORS MUST CHECK ALL DIMENSIONS ON SITE. ONLY FIGURED DIMENSIONS ARE TO BE WORKED FROM. DISCREPANCIES MUST BE REPORTED IMMEDIATELY TO ARCHITECT , S.O.,DESIGNER & CLIENT BEFORE PROCEEDING. | PROJECT<br>LOT 26662 – BUKIT BARU SALES GALLERY<br><br><b>MAIN LOBBY<br/>INTERIOR DETAILS</b> | SCALE   | AS SHOWN | DRAWING TITLE<br><b>FURNITURE, GARDEN SEATING &amp; ADVERTISING BOARD DECO</b> | REVISION |
|  |   |                                                                                               | DRAWN   | ALIAA    |                                                                                |          |
|  |   |                                                                                               | CHECKED | AMIN     | DRAWING NO<br><b>01</b>                                                        | 01       |
|  |   |                                                                                               | DATE    | 31/07/26 |                                                                                |          |

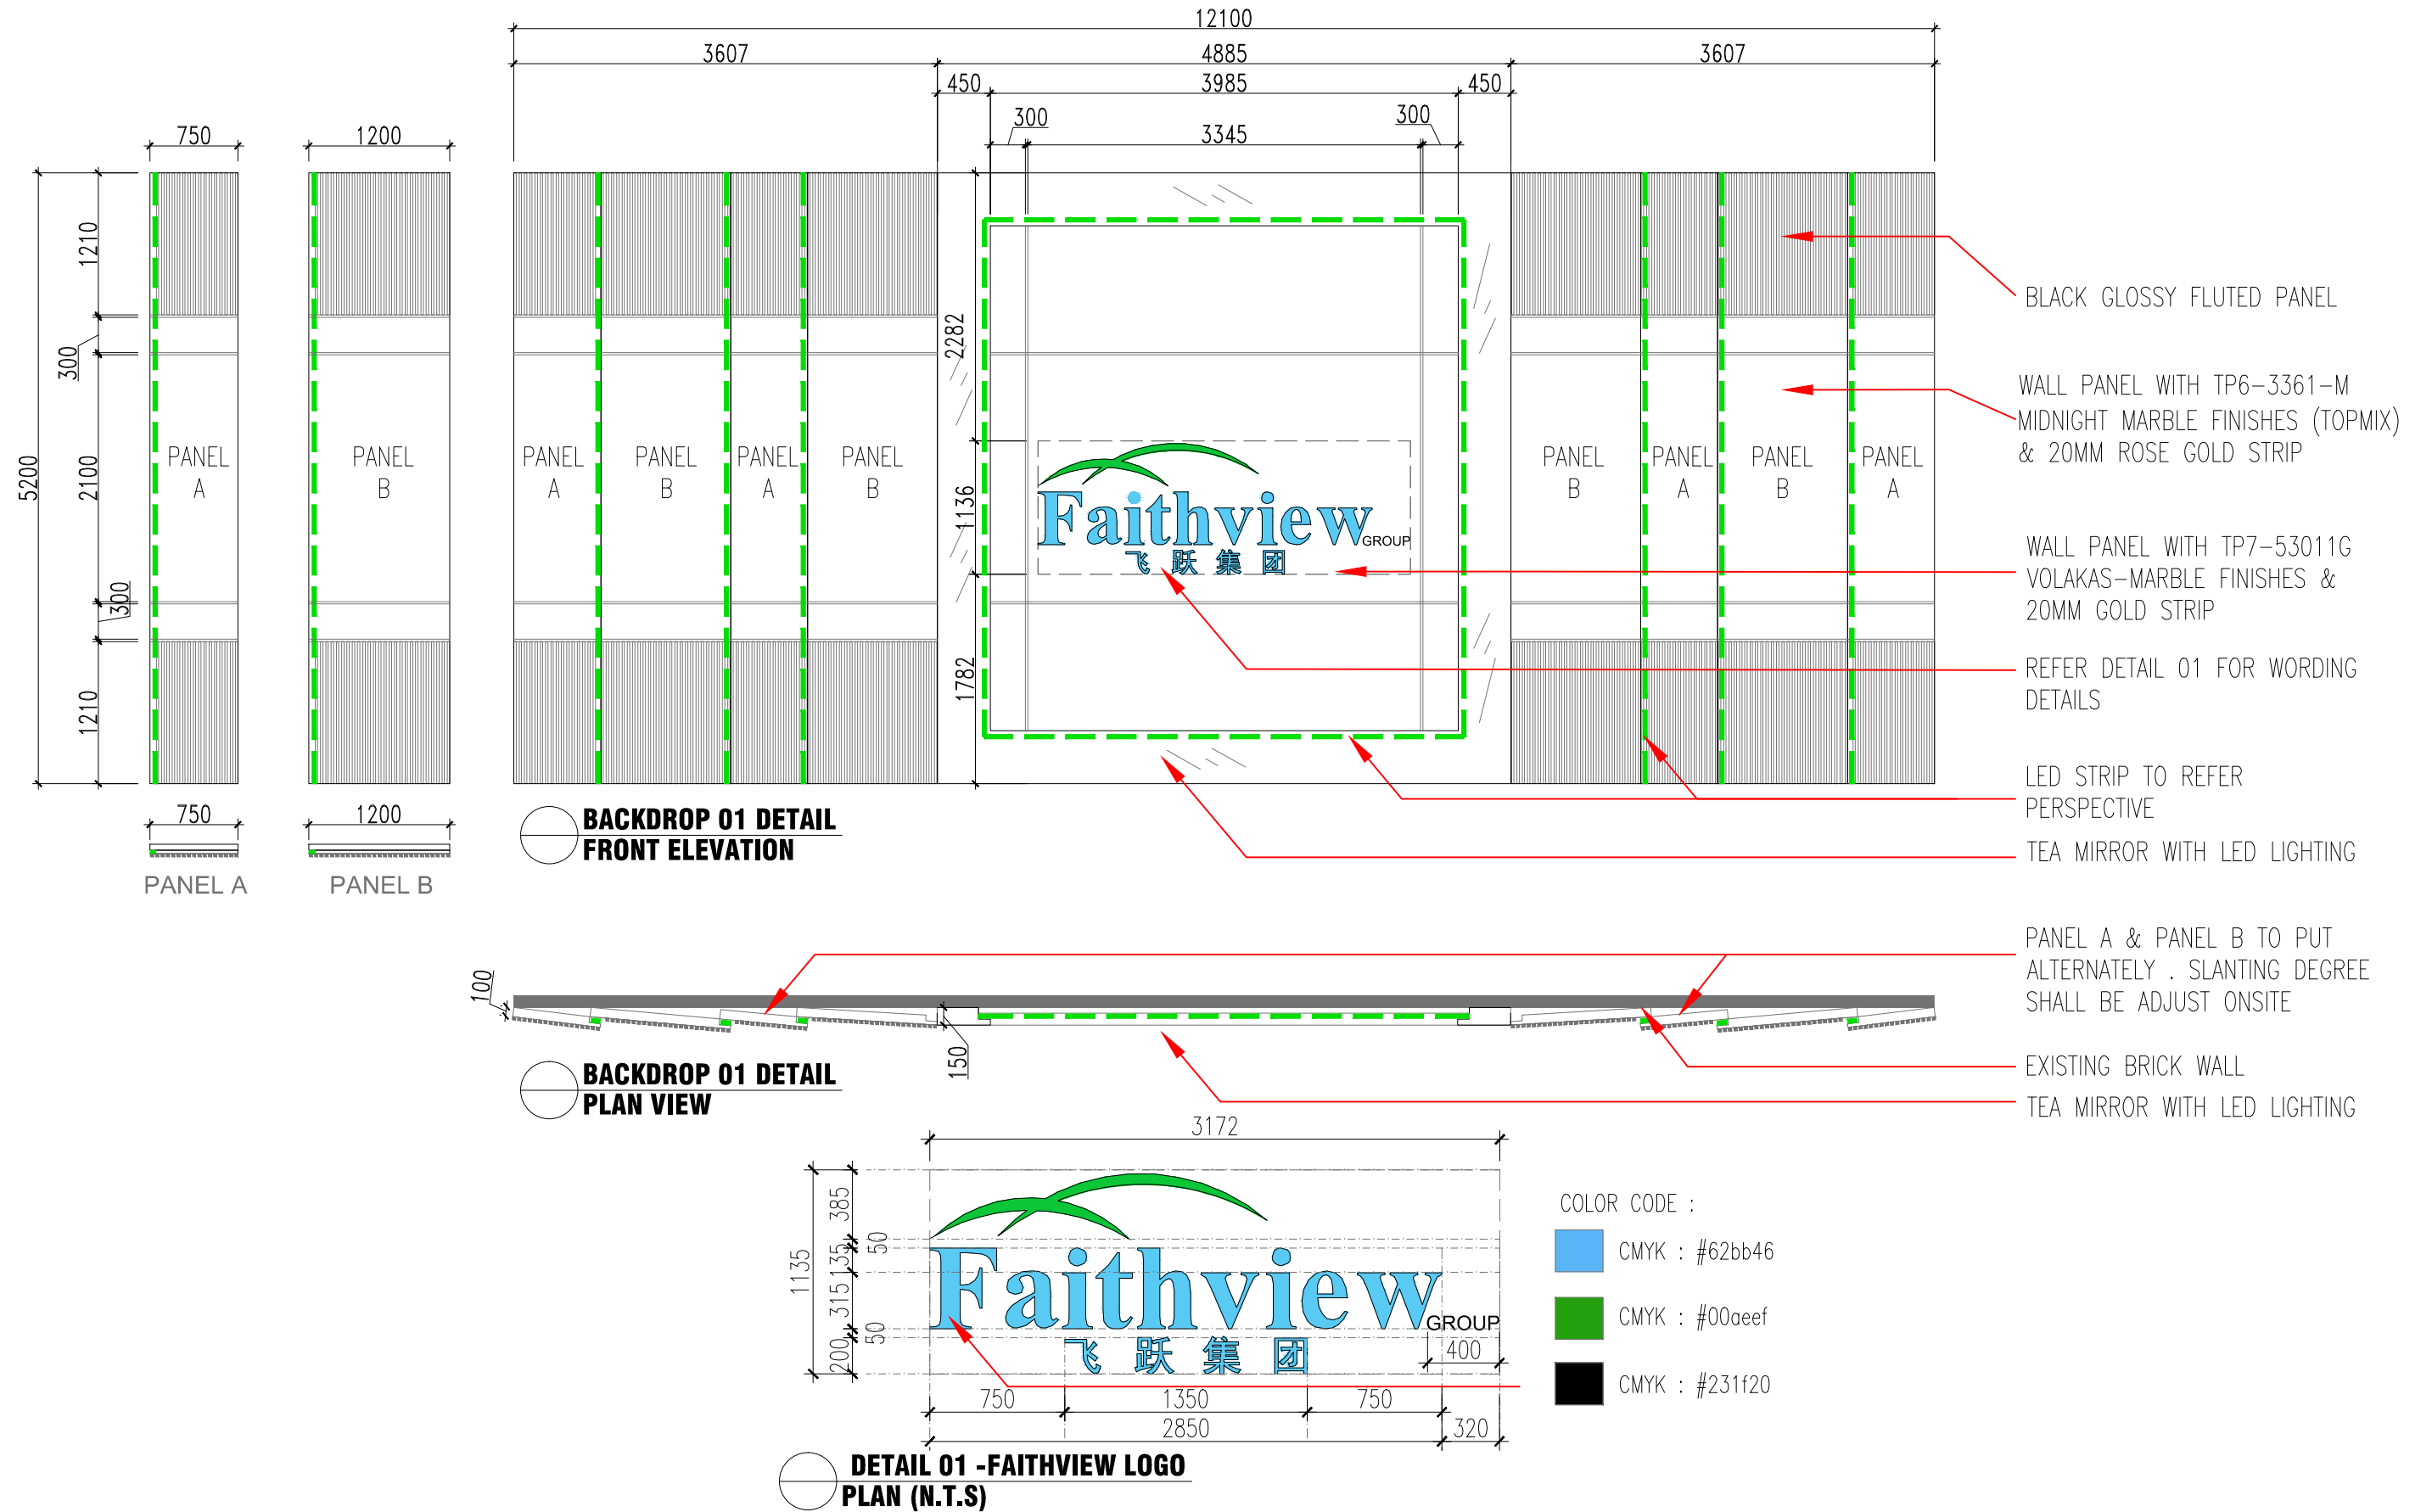


|  |   |                                                                                               |         |          |                            |          |
|--|---|-----------------------------------------------------------------------------------------------|---------|----------|----------------------------|----------|
|  | THIS DRAWING IS COPYRIGHTED. CONTRACTORS MUST CHECK ALL DIMENSIONS ON SITE. ONLY FIGURED DIMENSIONS ARE TO BE WORKED FROM. DISCREPANCIES MUST BE REPORTED IMMEDIATELY TO ARCHITECT , S.O., DESIGNER & CLIENT BEFORE PROCEEDING. | PROJECT<br>LOT 26662 - BUKIT BARU SALES GALLERY<br><br><b>MAIN LOBBY<br/>INTERIOR DETAILS</b> | SCALE   | AS SHOWN | DRAWING TITLE              | REVISION |
|  |   |                                                                                               | DRAWN   | ALIAA    | <b>BACKDROP 01 DETAILS</b> |          |
|  |   |                                                                                               | CHECKED | AMIN     | DRAWING NO                 | 01       |
|  |   |                                                                                               | DATE    | 20/07/26 | <b>02</b>                  |          |

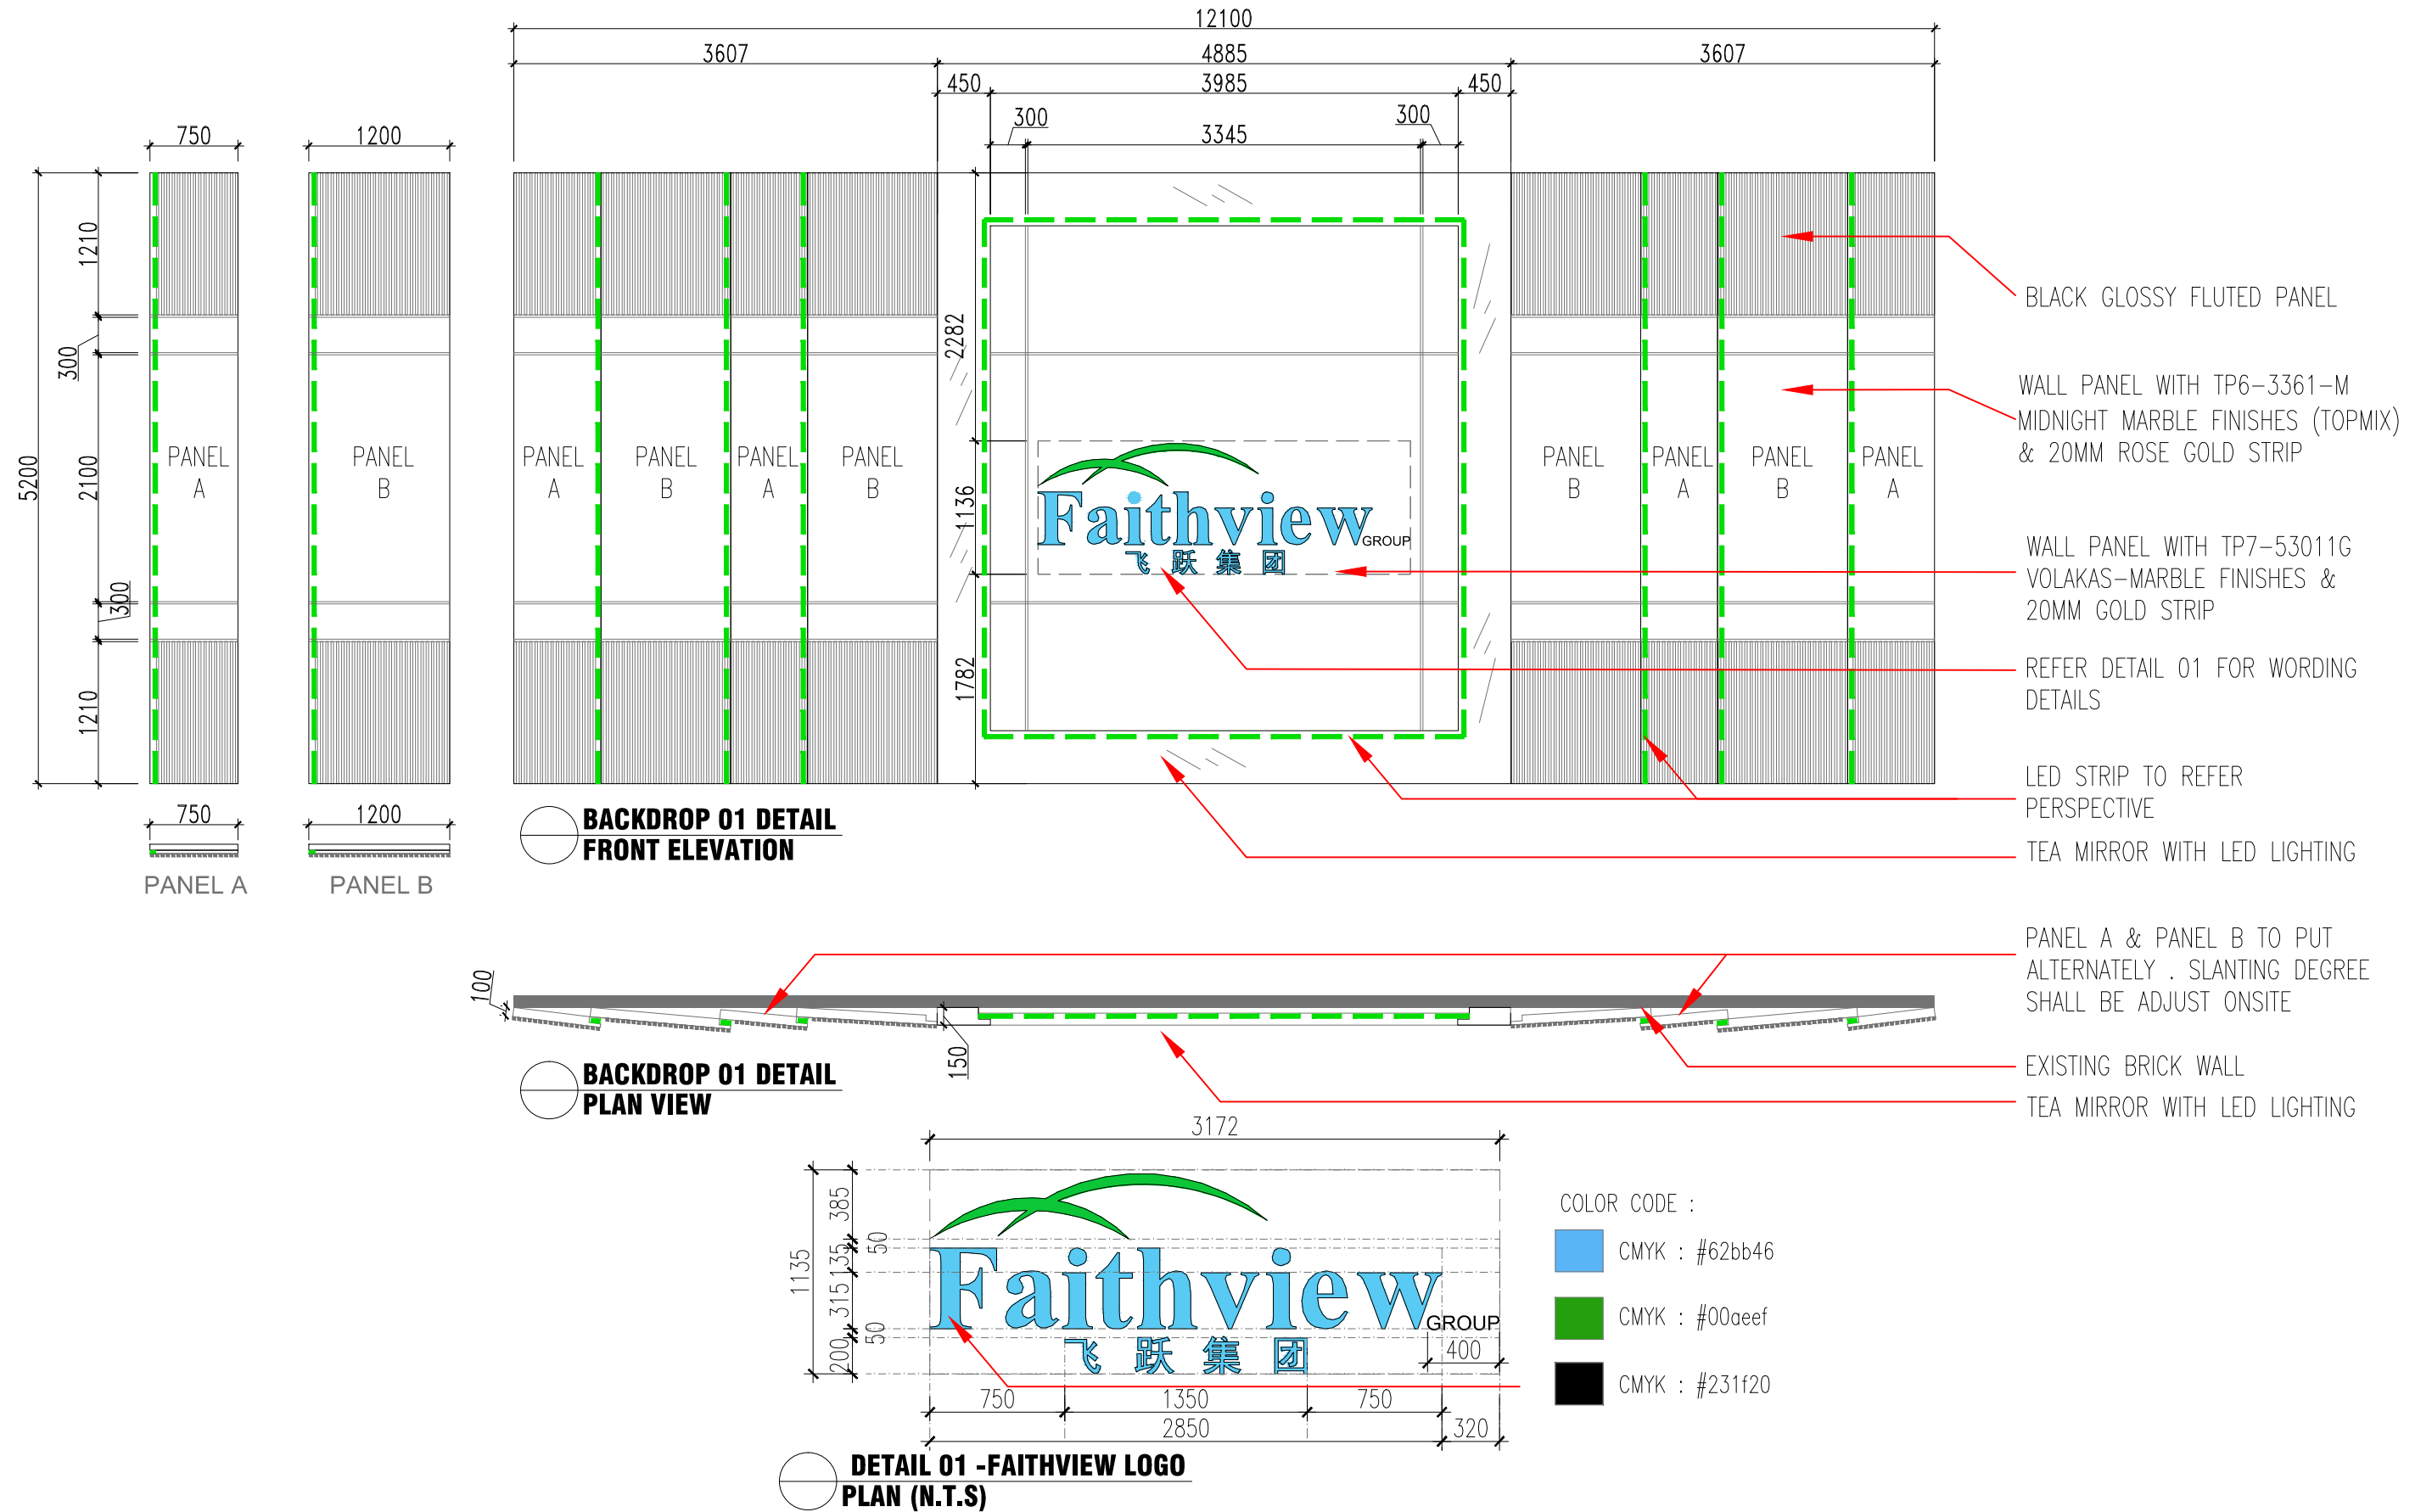

|  |   |                                                                                               |         |          |                            |          |
|--|---|-----------------------------------------------------------------------------------------------|---------|----------|----------------------------|----------|
|  | THIS DRAWING IS COPYRIGHTED. CONTRACTORS MUST CHECK ALL DIMENSIONS ON SITE. ONLY FIGURED DIMENSIONS ARE TO BE WORKED FROM. DISCREPANCIES MUST BE REPORTED IMMEDIATELY TO ARCHITECT , S.O.,DESIGNER & CLIENT BEFORE PROCEEDING. | PROJECT<br>LOT 26662 – BUKIT BARU SALES GALLERY<br><br><b>MAIN LOBBY<br/>INTERIOR DETAILS</b> | SCALE   | AS SHOWN | DRAWING TITLE              | REVISION |
|  |   |                                                                                               | DRAWN   | ALIAA    | <b>BACKDROP 01 DETAILS</b> |          |
|  |   |                                                                                               | CHECKED | AMIN     | DRAWING NO                 | 01       |
|  |   |                                                                                               | DATE    | 20/07/26 | <b>02</b>                  |          |

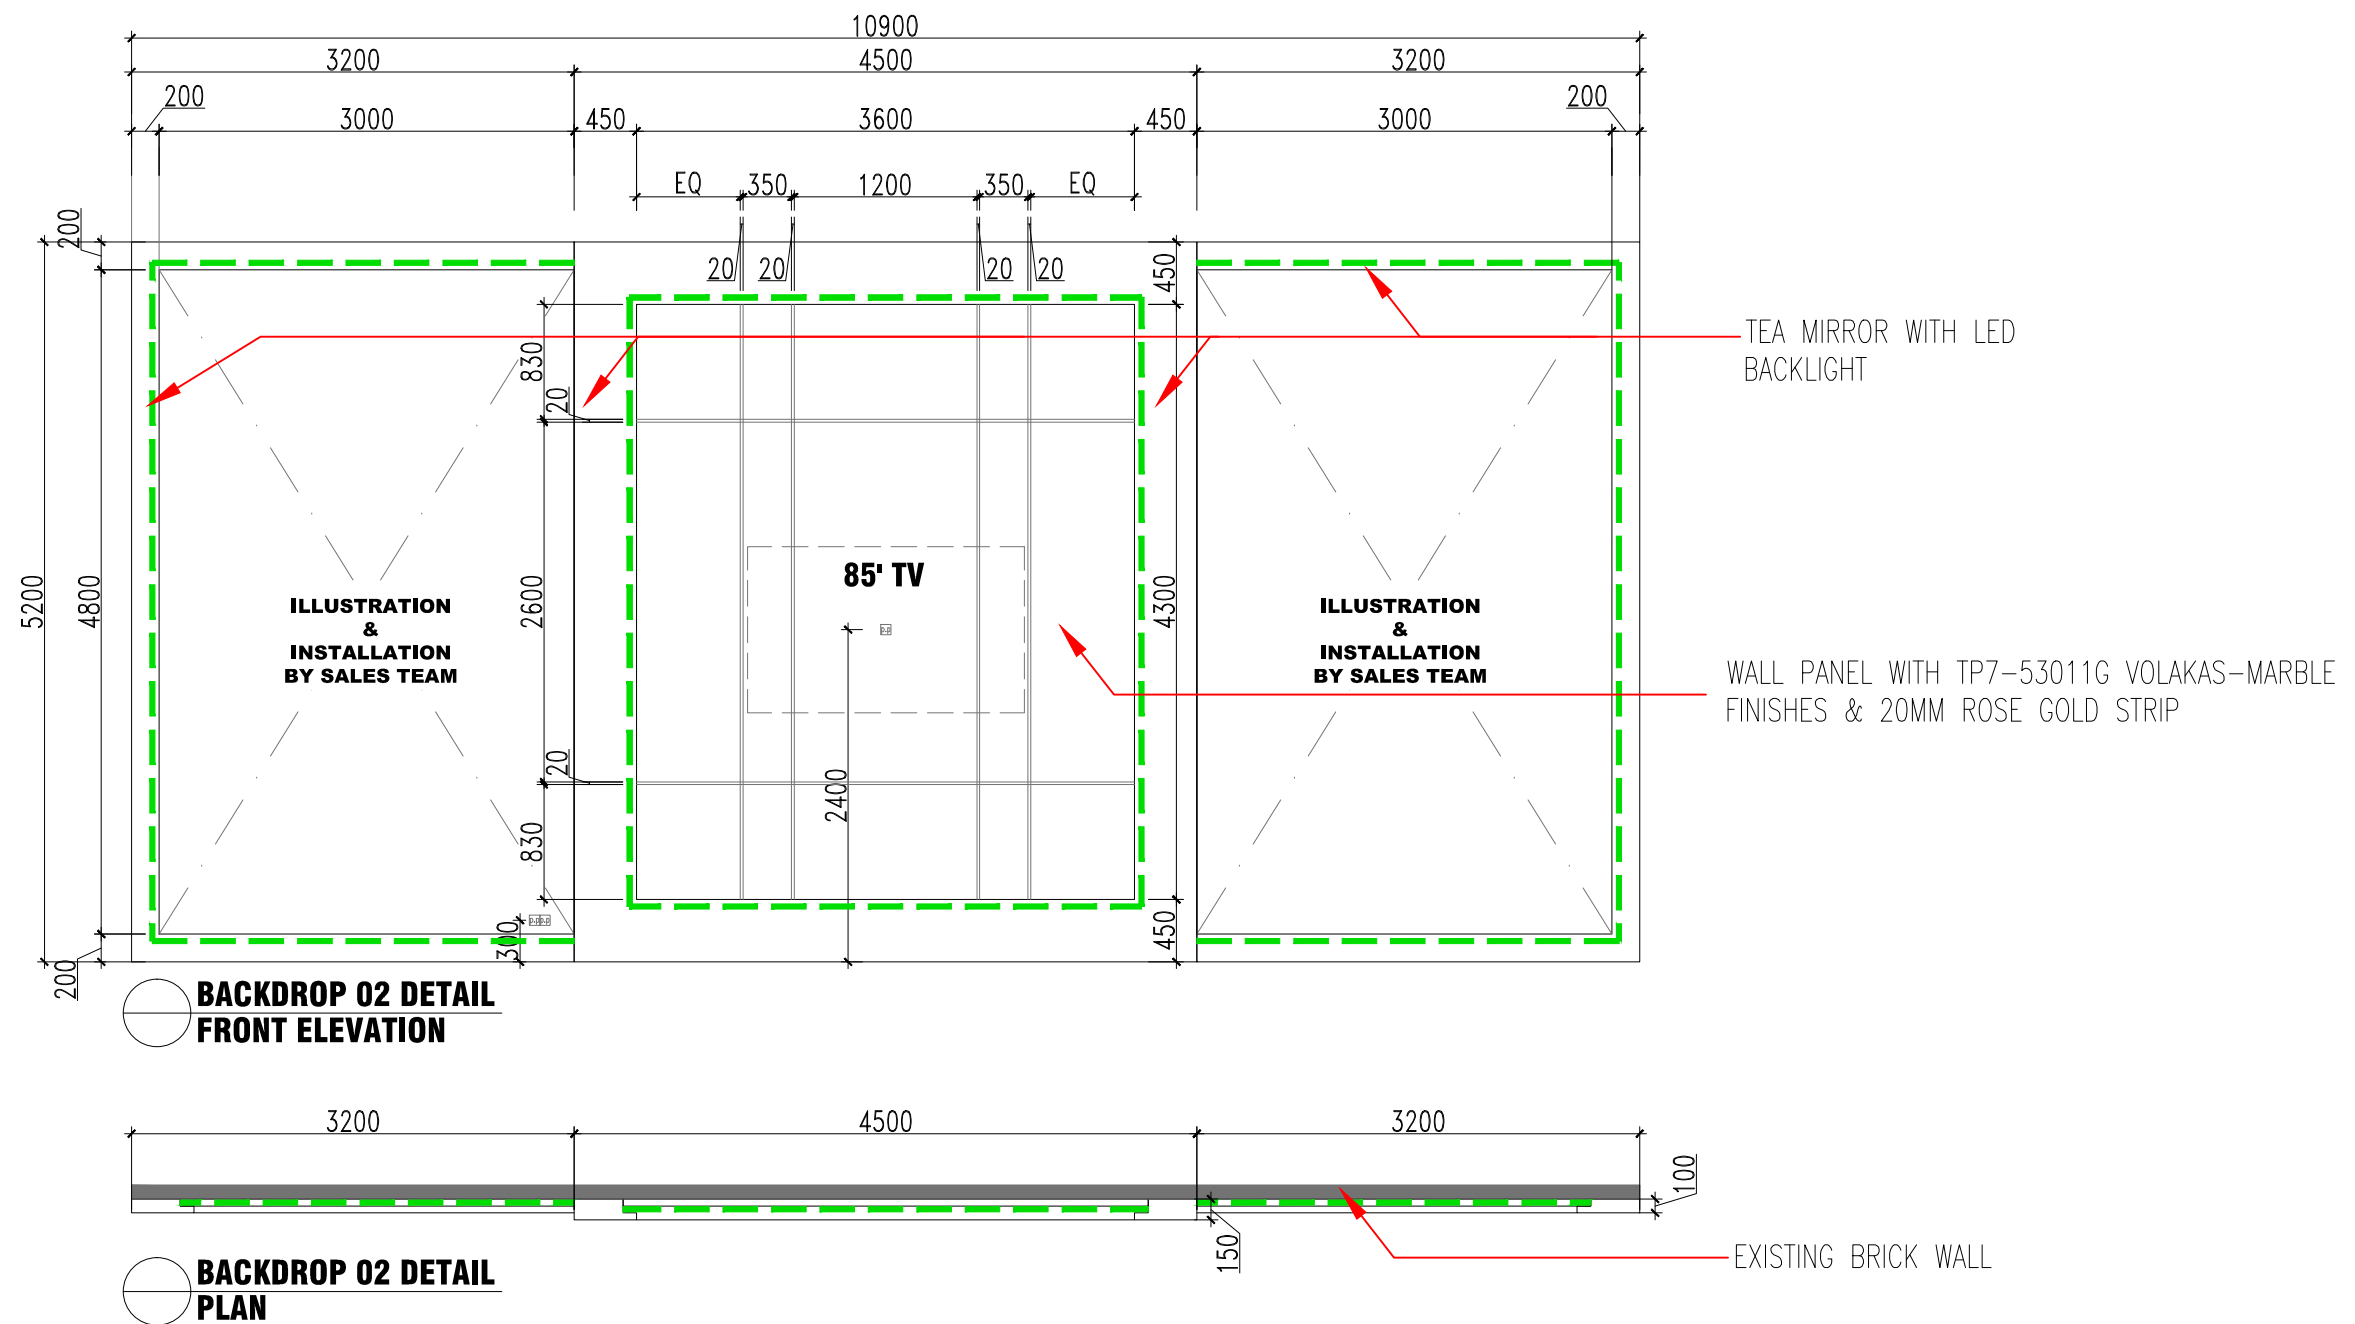

|  |   |                                                                                               |         |          |                            |          |
|--|---|-----------------------------------------------------------------------------------------------|---------|----------|----------------------------|----------|
|  | THIS DRAWING IS COPYRIGHTED. CONTRACTORS MUST CHECK ALL DIMENSIONS ON SITE. ONLY FIGURED DIMENSIONS ARE TO BE WORKED FROM. DISCREPANCIES MUST BE REPORTED IMMEDIATELY TO ARCHITECT , S.O.,DESIGNER & CLIENT BEFORE PROCEEDING. | PROJECT<br>LOT 26662 – BUKIT BARU SALES GALLERY<br><br><b>MAIN LOBBY<br/>INTERIOR DETAILS</b> | SCALE   | AS SHOWN | DRAWING TITLE              | REVISION |
|  |   |                                                                                               | DRAWN   | ALIAA    | <b>BACKDROP 02 DETAILS</b> |          |
|  |   |                                                                                               | CHECKED | AMIN     | DRAWING NO                 | 01       |
|  |   |                                                                                               | DATE    | 20/07/26 | <b>03</b>                  |          |

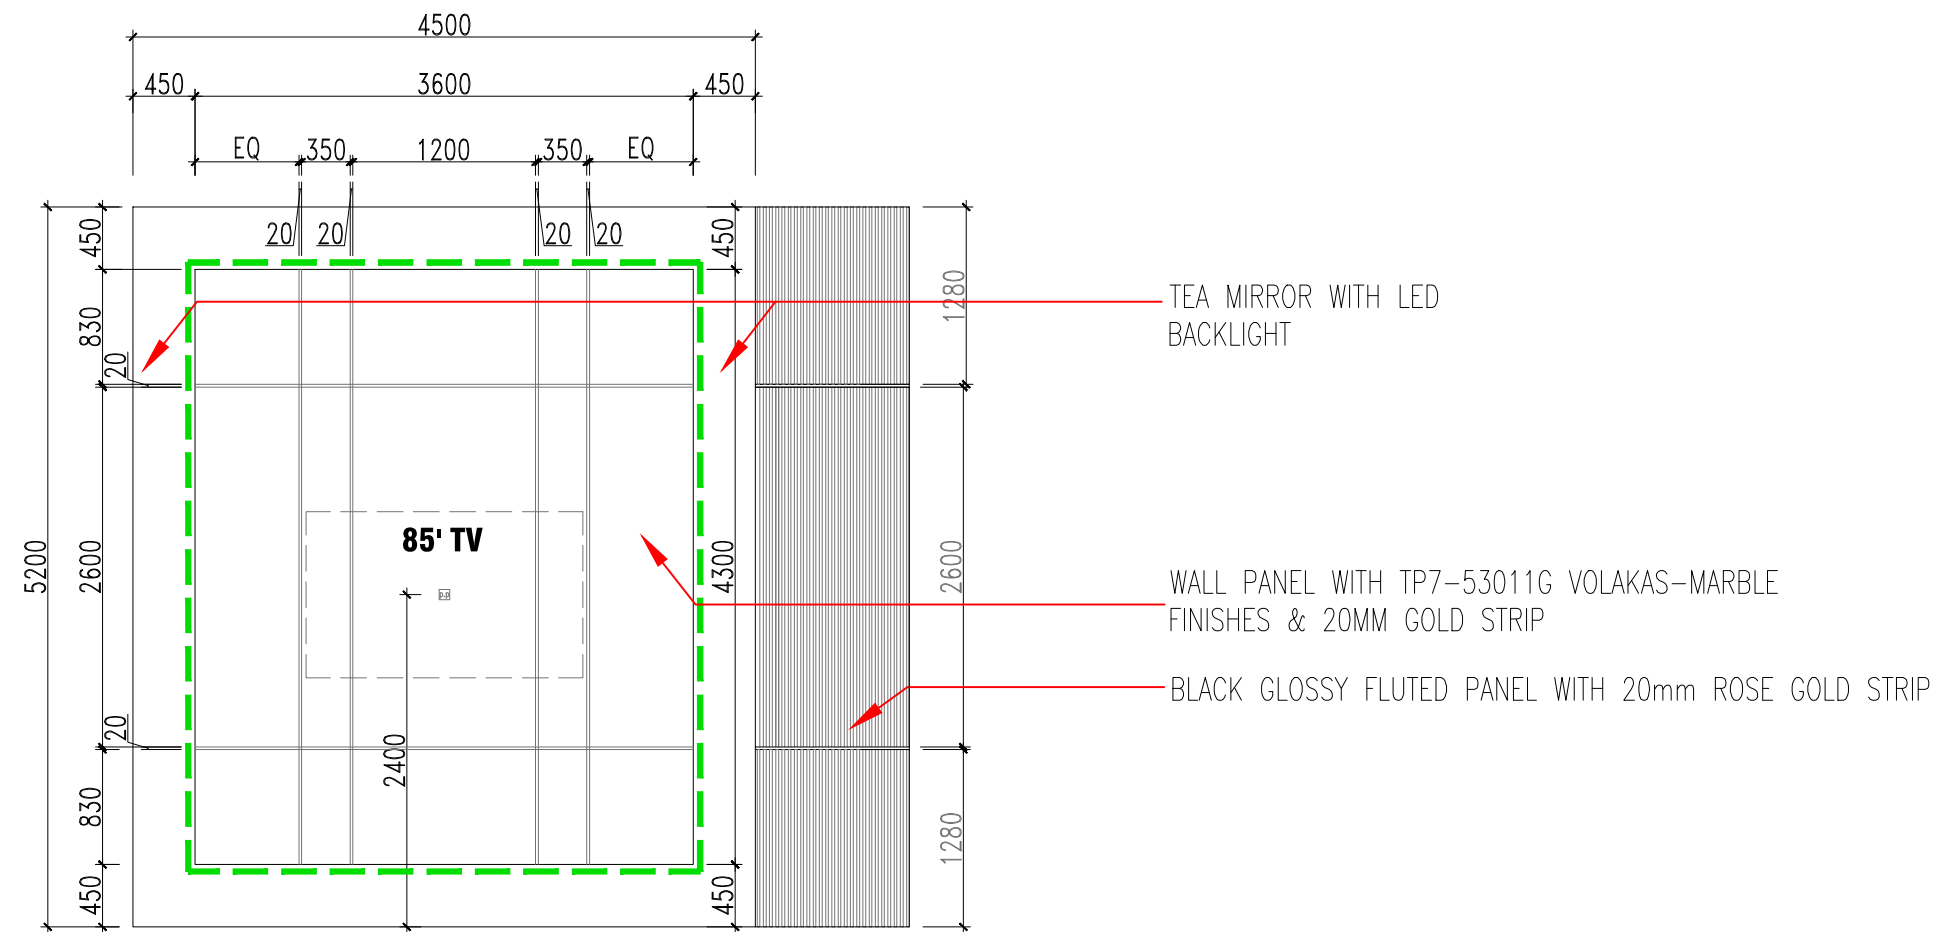


**BACKDROP 03 DETAIL  
FRONT ELEVATION**



**BACKDROP 03 DETAIL  
PLAN**


|  |   |                                                                                               |         |          |                                             |                    |
|--|---|-----------------------------------------------------------------------------------------------|---------|----------|---------------------------------------------|--------------------|
|  | THIS DRAWING IS COPYRIGHTED. CONTRACTORS MUST CHECK ALL DIMENSIONS ON SITE. ONLY FIGURED DIMENSIONS ARE TO BE WORKED FROM. DISCREPANCIES MUST BE REPORTED IMMEDIATELY TO ARCHITECT , S.O.,DESIGNER & CLIENT BEFORE PROCEEDING. | PROJECT<br>LOT 26662 – BUKIT BARU SALES GALLERY<br><br><b>MAIN LOBBY<br/>INTERIOR DETAILS</b> | SCALE   | AS SHOWN | DRAWING TITLE<br><b>BACKDROP 03 DETAILS</b> | REVISION<br><br>01 |
|  |   |                                                                                               | DRAWN   | ALIAA    |                                             |                    |
|  |   |                                                                                               | CHECKED | AMIN     | DRAWING NO<br><b>04</b>                     |                    |
|  |   |                                                                                               | DATE    | 31/07/26 |                                             |                    |

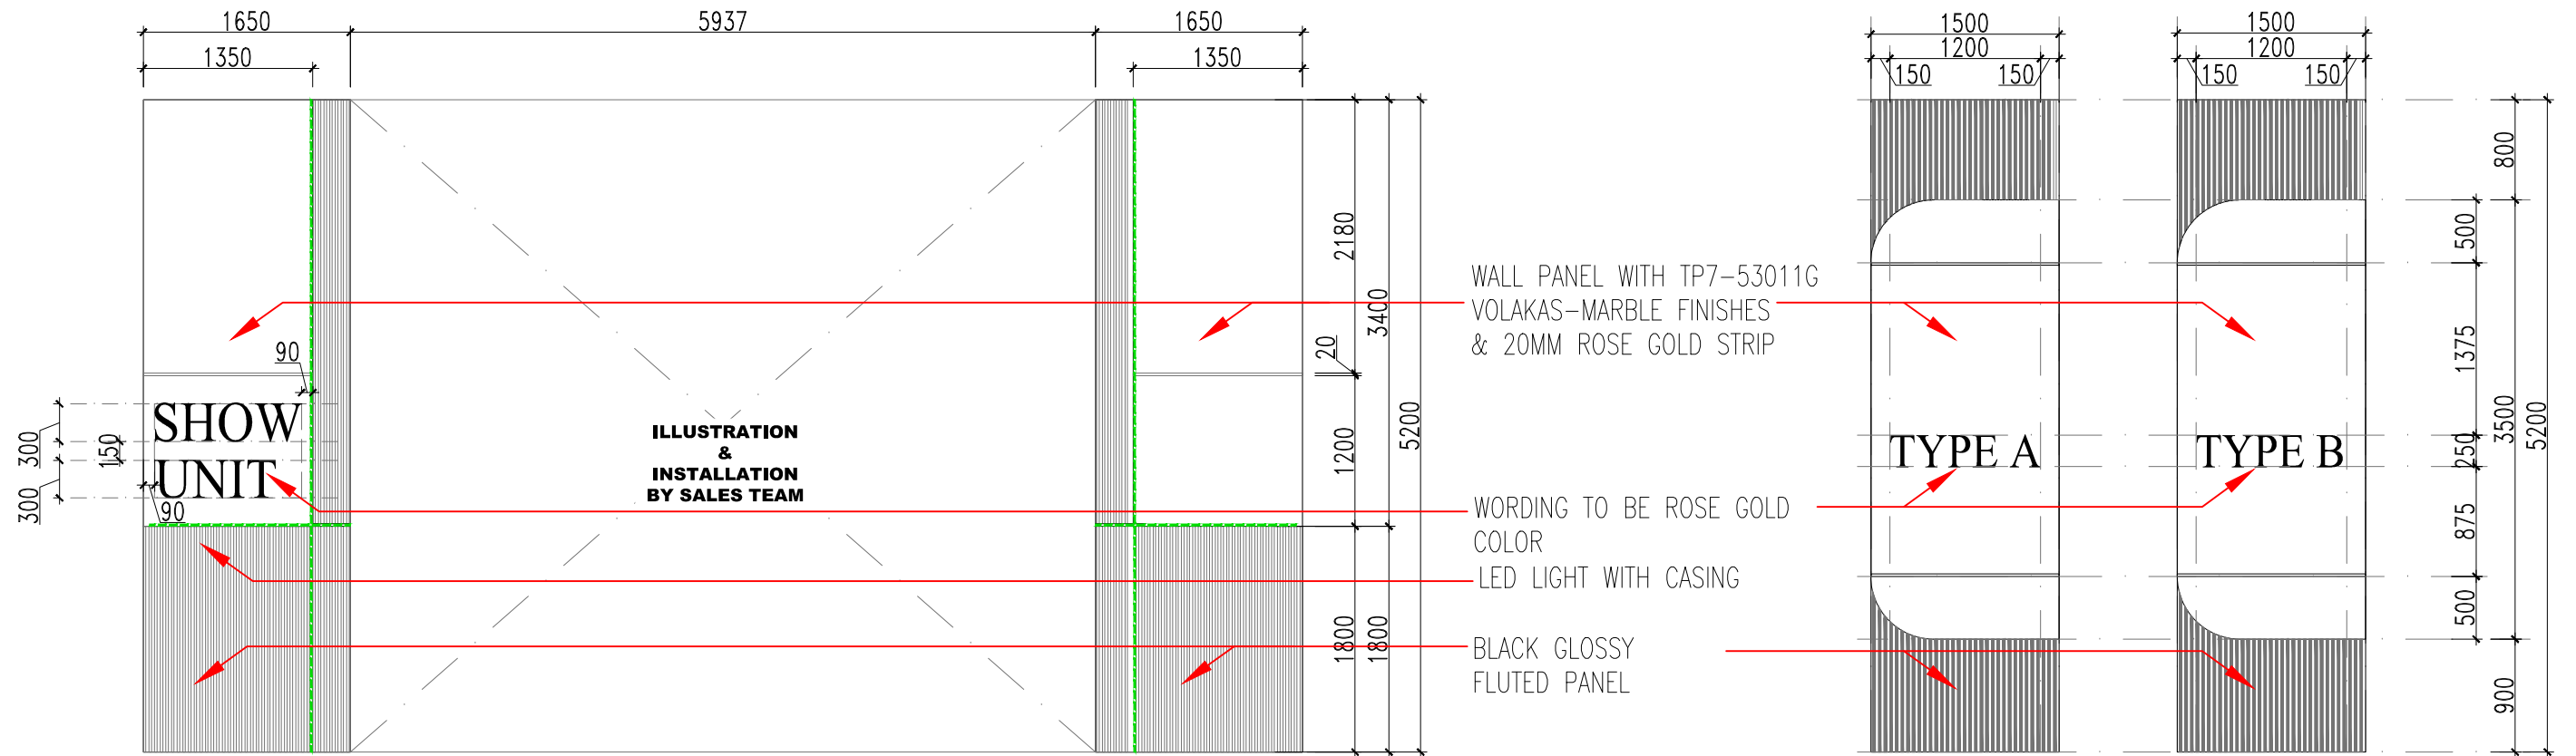

BACKDROP 04 DETAIL  
FRONT ELEVATION

BACKDROP 04 DETAIL  
PLAN



SHOW UNIT SIGNAGE  
PLAN

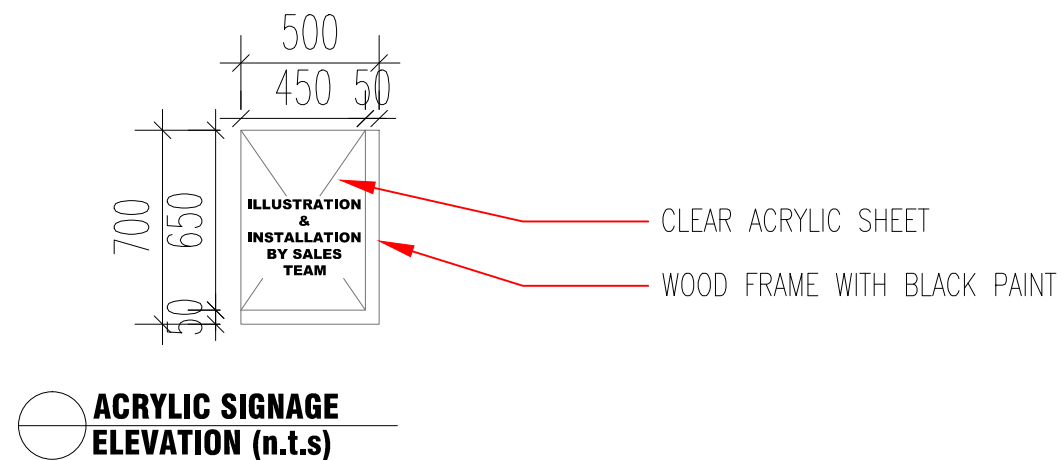



ACRYLIC SIGNAGE  
ELEVATION (n.t.s)

|  |   |                                                                                               |         |          |                                                                     |          |
|--|---|-----------------------------------------------------------------------------------------------|---------|----------|---------------------------------------------------------------------|----------|
|  | THIS DRAWING IS COPYRIGHTED. CONTRACTORS MUST CHECK ALL DIMENSIONS ON SITE. ONLY FIGURED DIMENSIONS ARE TO BE WORKED FROM. DISCREPANCIES MUST BE REPORTED IMMEDIATELY TO ARCHITECT , S.O.,DESIGNER & CLIENT BEFORE PROCEEDING. | PROJECT<br>LOT 26662 – BUKIT BARU SALES GALLERY<br><br><b>MAIN LOBBY<br/>INTERIOR DETAILS</b> | SCALE   | AS SHOWN | DRAWING TITLE                                                       | REVISION |
|  |   |                                                                                               | DRAWN   | ALIAA    | <b>BACKDROP 04 , TYP.UNIT SIGNAGE DETAILS &amp; ACRYLIC SIGNAGE</b> |          |
|  |   |                                                                                               | CHECKED | AMIN     | DRAWING NO                                                          | 01       |
|  |   |                                                                                               | DATE    | 20/07/26 | <b>05</b>                                                           |          |




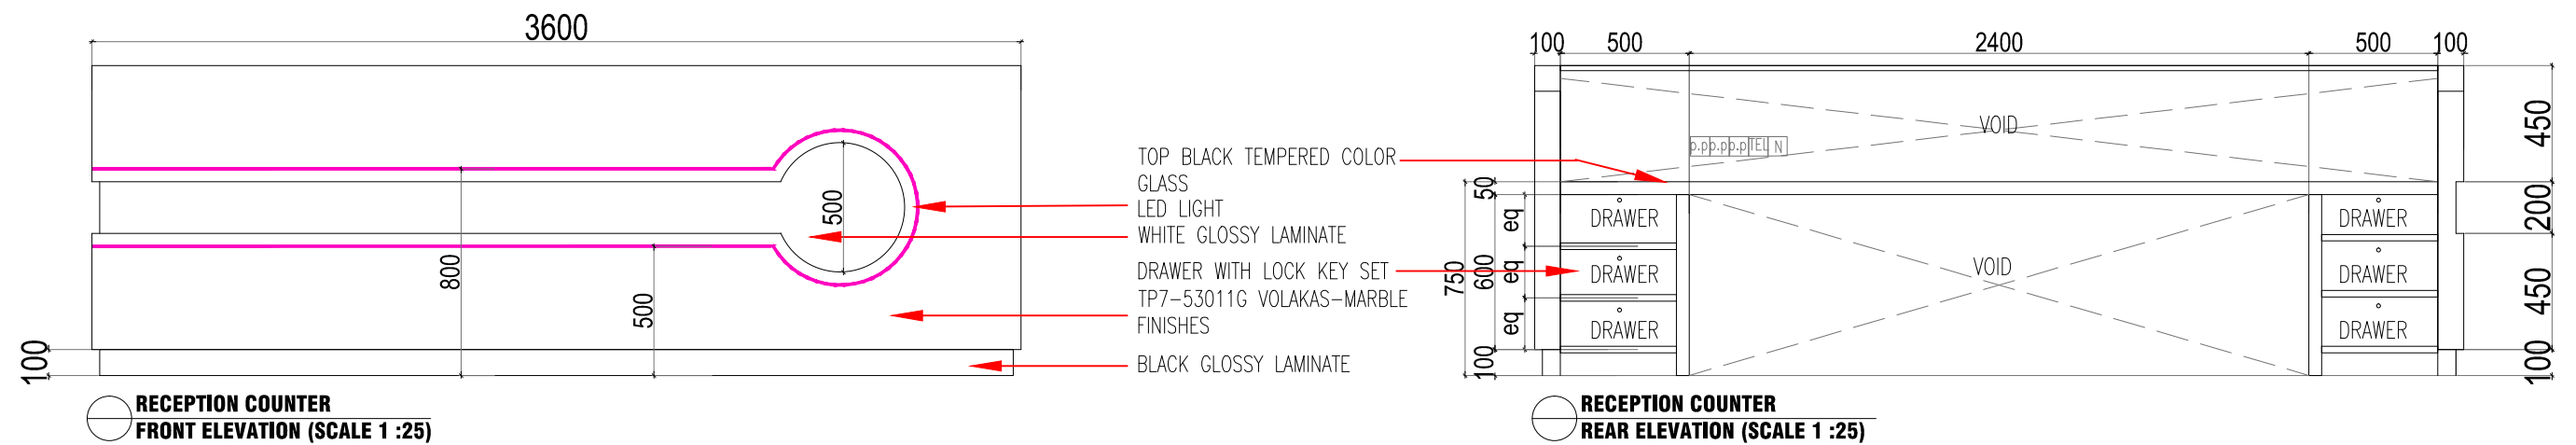
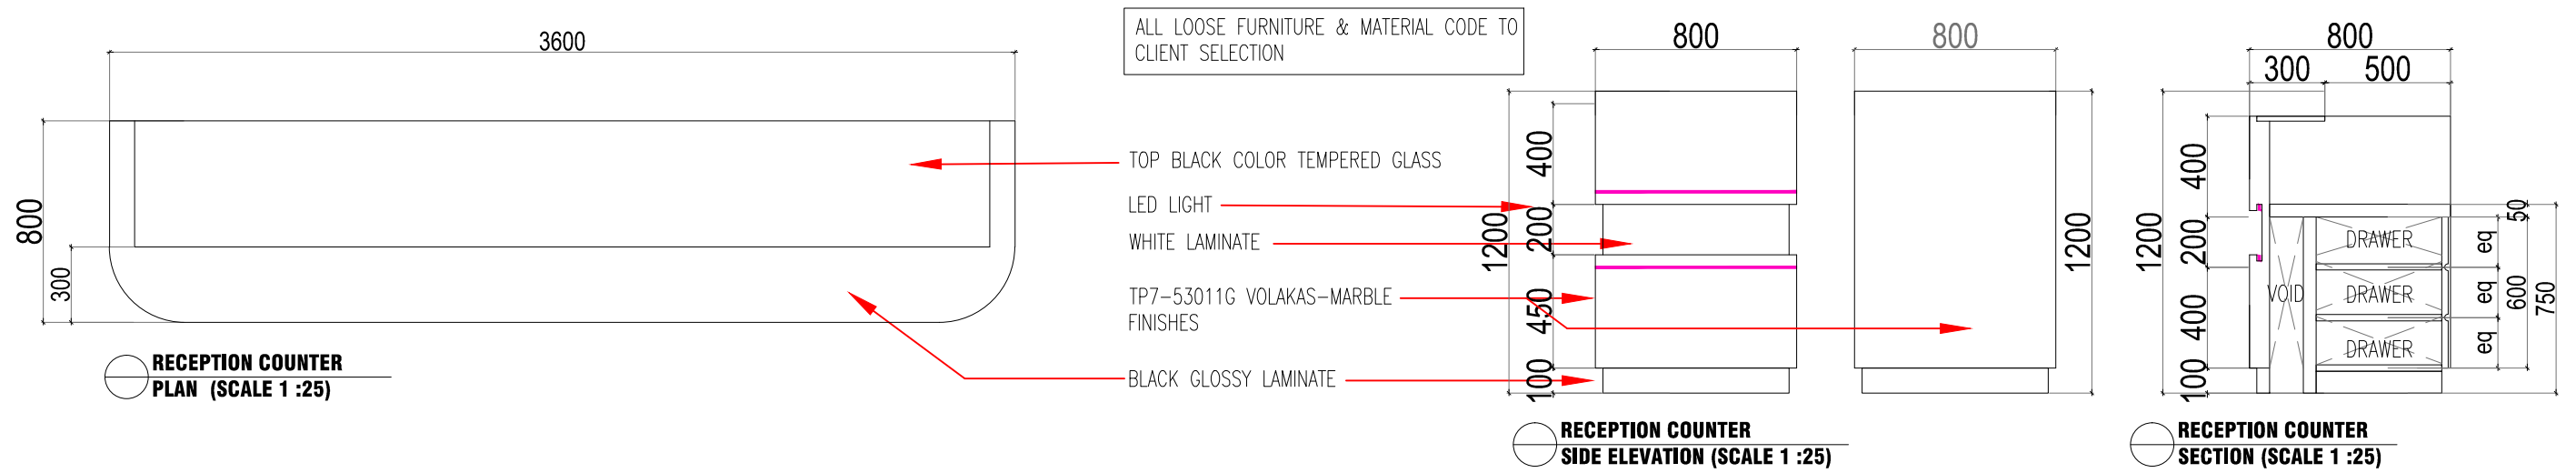


|  |   |                                                                                               |         |          |                                                  |                                      |
|--|---|-----------------------------------------------------------------------------------------------|---------|----------|--------------------------------------------------|--------------------------------------|
|  | THIS DRAWING IS COPYRIGHTED. CONTRACTORS MUST CHECK ALL DIMENSIONS ON SITE. ONLY FIGURED DIMENSIONS ARE TO BE WORKED FROM. DISCREPANCIES MUST BE REPORTED IMMEDIATELY TO ARCHITECT , S.O.,DESIGNER & CLIENT BEFORE PROCEEDING. | PROJECT<br>LOT 26662 – BUKIT BARU SALES GALLERY<br><br><b>MAIN LOBBY<br/>INTERIOR DETAILS</b> | SCALE   | AS SHOWN | DRAWING TITLE<br><b>RECEPTION COUNTER DETAIL</b> | REVISION                             |
|  |   |                                                                                               | DRAWN   | ALIAA    |                                                  |                                      |
|  |   |                                                                                               | CHECKED | AMIN     | DRAWING NO<br><b>06</b>                          | <div> <div></div> <div></div> </div> |
|  |   |                                                                                               | DATE    | 10/07/26 |                                                  |                                      |

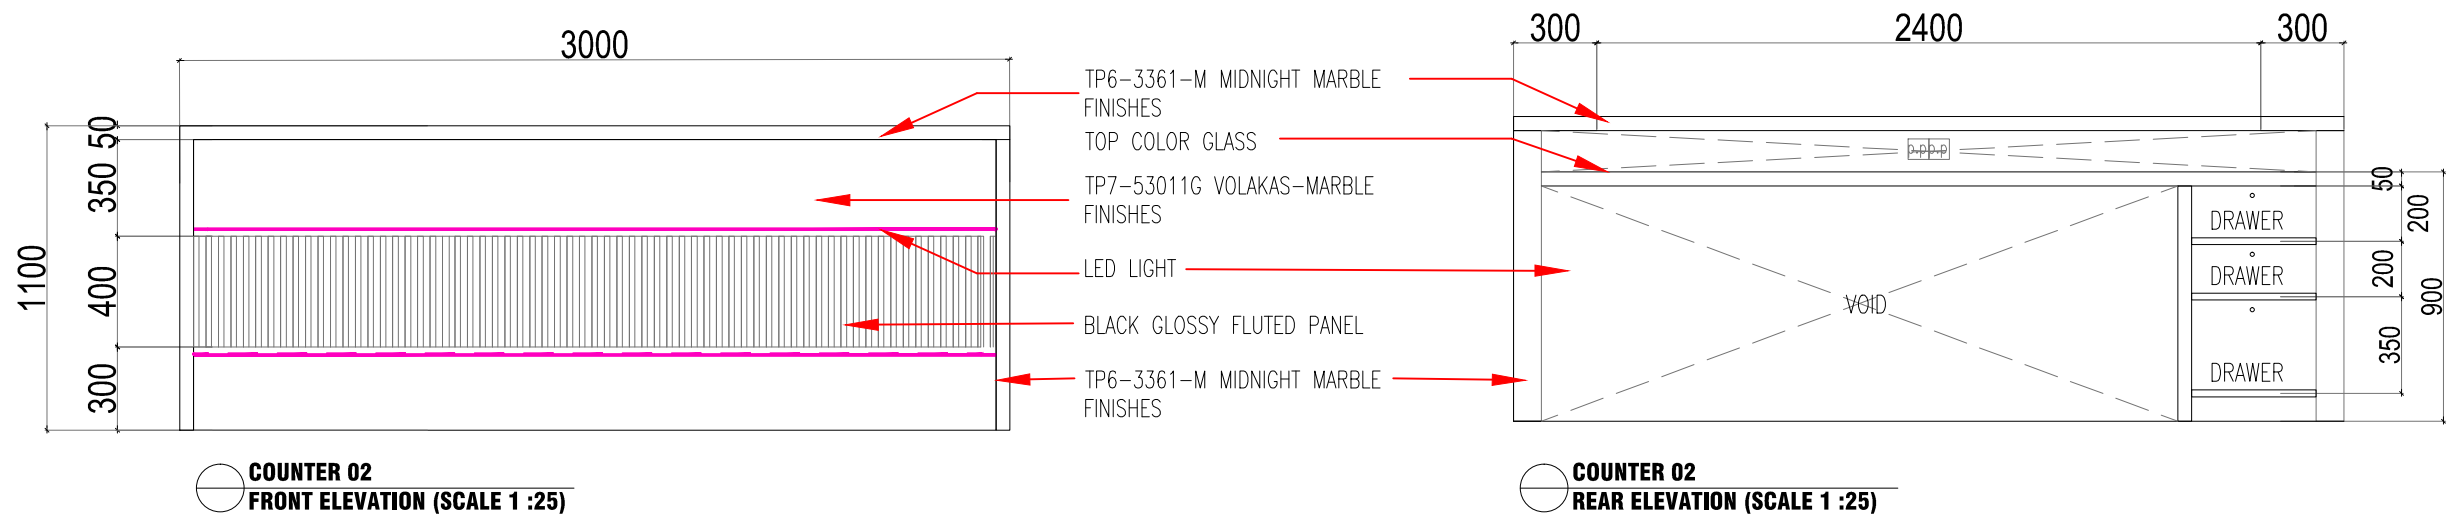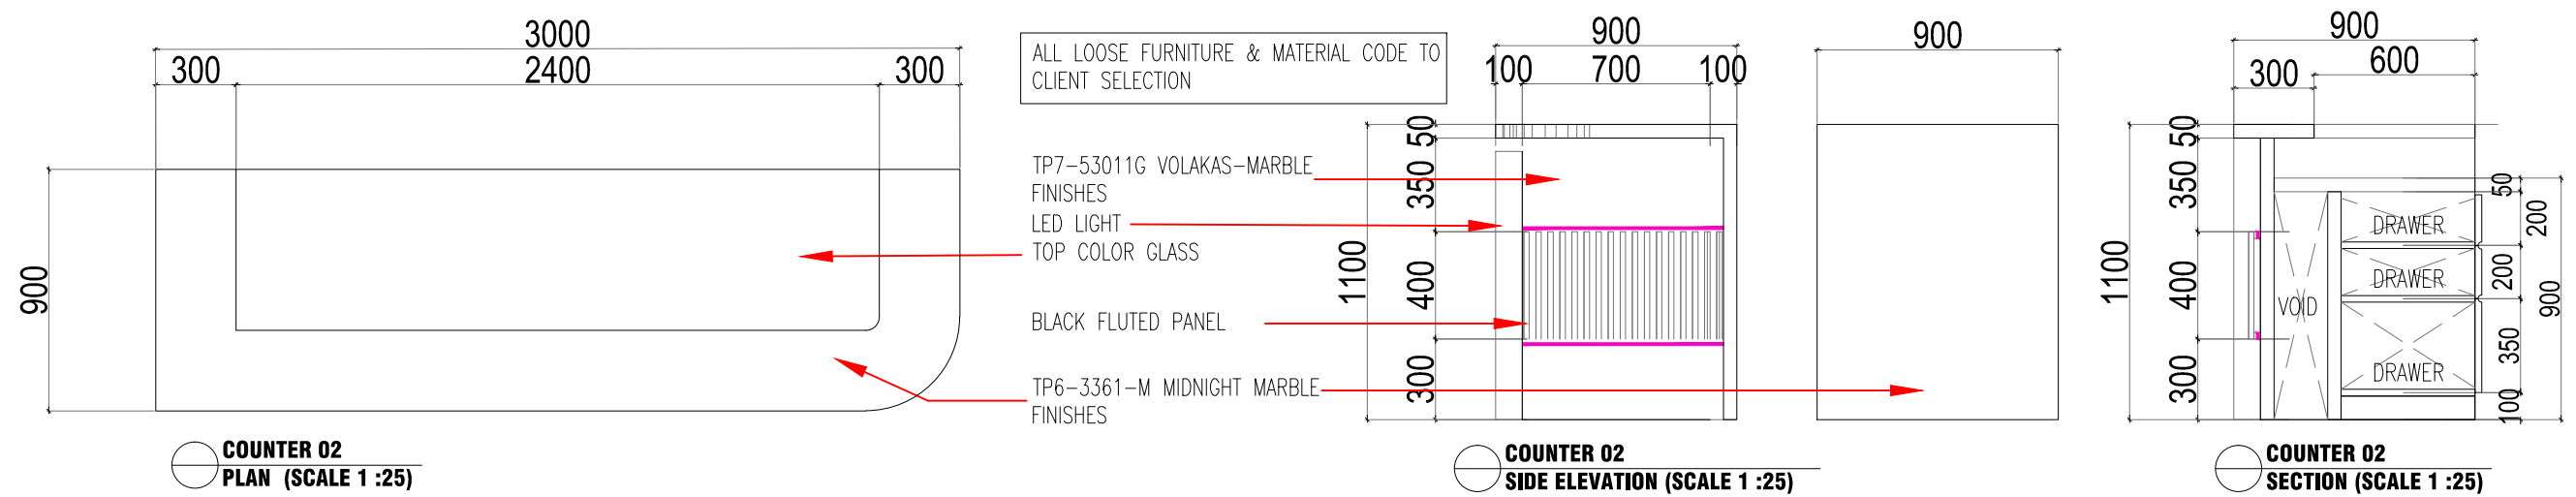


|  |   |                                                                                               |         |          |                                           |                           |
|--|---|-----------------------------------------------------------------------------------------------|---------|----------|-------------------------------------------|---------------------------|
|  | THIS DRAWING IS COPYRIGHTED. CONTRACTORS MUST CHECK ALL DIMENSIONS ON SITE. ONLY FIGURED DIMENSIONS ARE TO BE WORKED FROM. DISCREPANCIES MUST BE REPORTED IMMEDIATELY TO ARCHITECT , S.O.,DESIGNER & CLIENT BEFORE PROCEEDING. | PROJECT<br>LOT 26662 – BUKIT BARU SALES GALLERY<br><br><b>MAIN LOBBY<br/>INTERIOR DETAILS</b> | SCALE   | AS SHOWN | DRAWING TITLE<br><b>COUNTER 02 DETAIL</b> | REVISION                  |
|  |   |                                                                                               | DRAWN   | ALIAA    |                                           |                           |
|  |   |                                                                                               | CHECKED | AMIN     | DRAWING NO<br><b>07</b>                   | <div>○</div> <div>○</div> |
|  |   |                                                                                               | DATE    | 10/07/26 |                                           |                           |



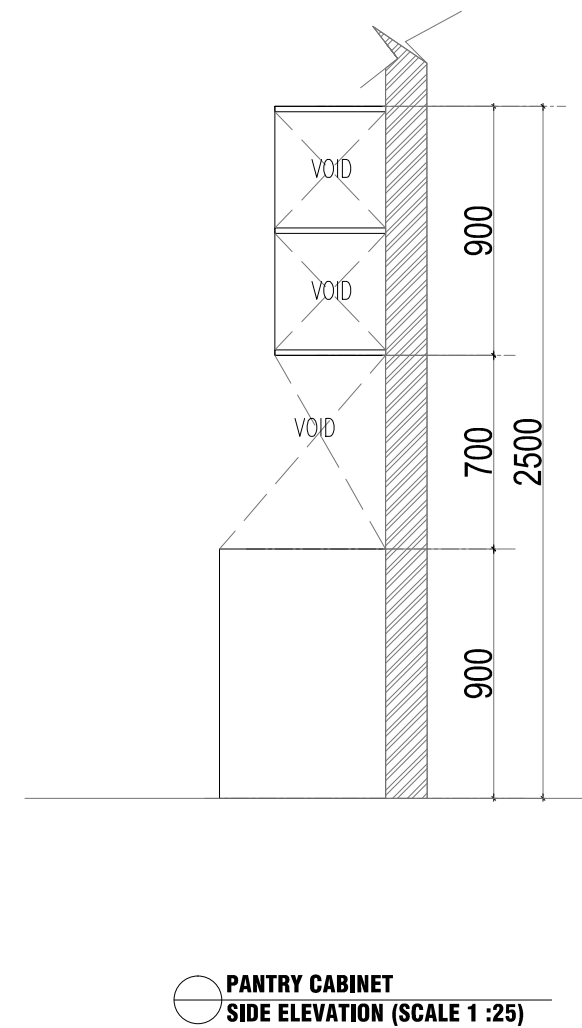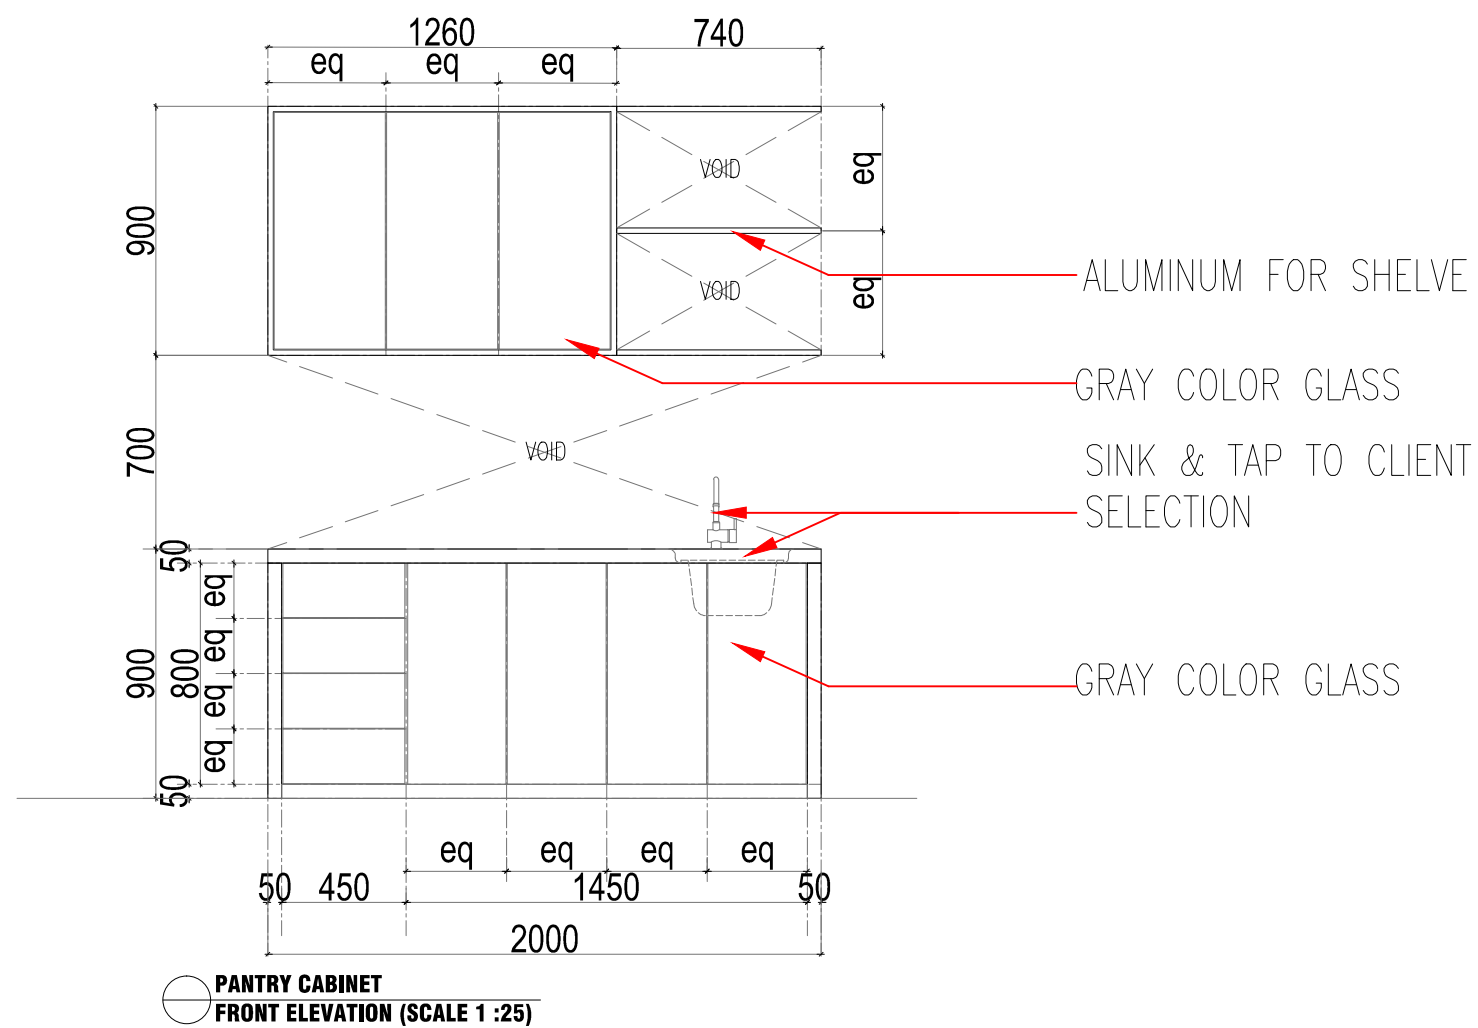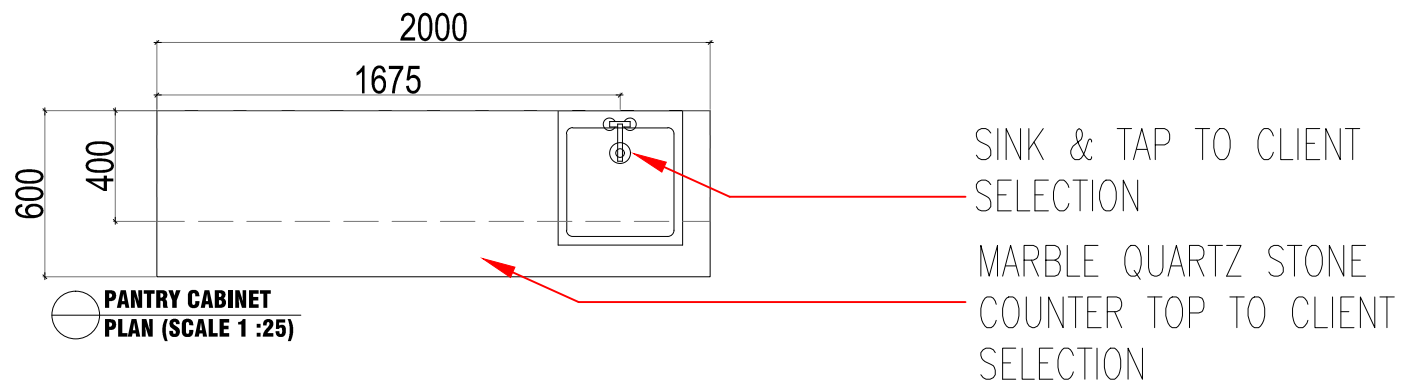


|  |   |                                                                                               |         |          |                                       |          |
|--|---|-----------------------------------------------------------------------------------------------|---------|----------|---------------------------------------|----------|
|  | THIS DRAWING IS COPYRIGHTED. CONTRACTORS MUST CHECK ALL DIMENSIONS ON SITE. ONLY FIGURED DIMENSIONS ARE TO BE WORKED FROM. DISCREPANCIES MUST BE REPORTED IMMEDIATELY TO ARCHITECT , S.O.,DESIGNER & CLIENT BEFORE PROCEEDING. | PROJECT<br>LOT 26662 – BUKIT BARU SALES GALLERY<br><br><b>MAIN LOBBY<br/>INTERIOR DETAILS</b> | SCALE   | AS SHOWN | DRAWING TITLE<br><b>PANTRY DETAIL</b> | REVISION |
|  |   |                                                                                               | DRAWN   | ALIAA    |                                       |          |
|  |   |                                                                                               | CHECKED | AMIN     | DRAWING NO<br><b>08</b>               | ○ ○      |
|  |   |                                                                                               | DATE    | 10/07/26 |                                       |          |

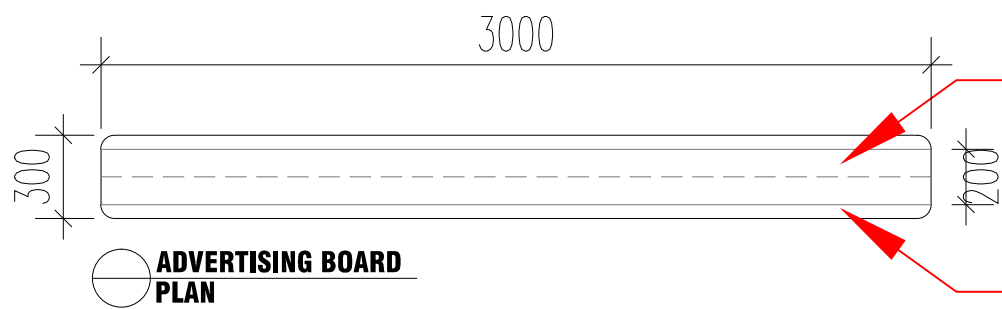

ADVERTISING BOARD  
PLAN


DOUBLE FRONTAGE LIGHTBOX PANEL  
WITH LED BACKLIGHTING, COMPLETE  
WITH BLACK LAMINATE BACKING AND  
FRAME, AND CONCEALED WIRING

3000 x 300 BASE WITH BLACK  
LAMINATE

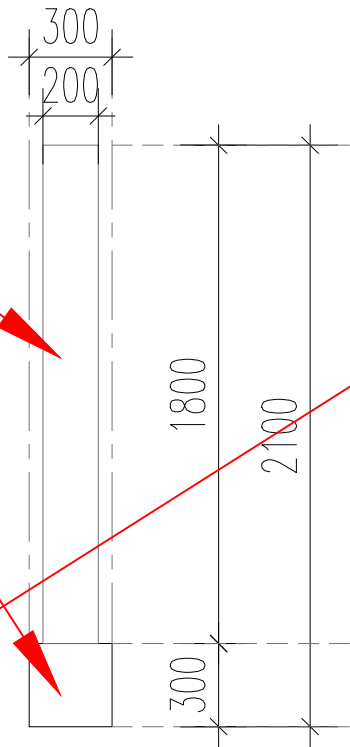

ADVERTISING BOARD  
SIDE ELEVATION

ALL LOOSE FURNITURE &  
MATERIAL CODE TO CLIENT  
SELECTION

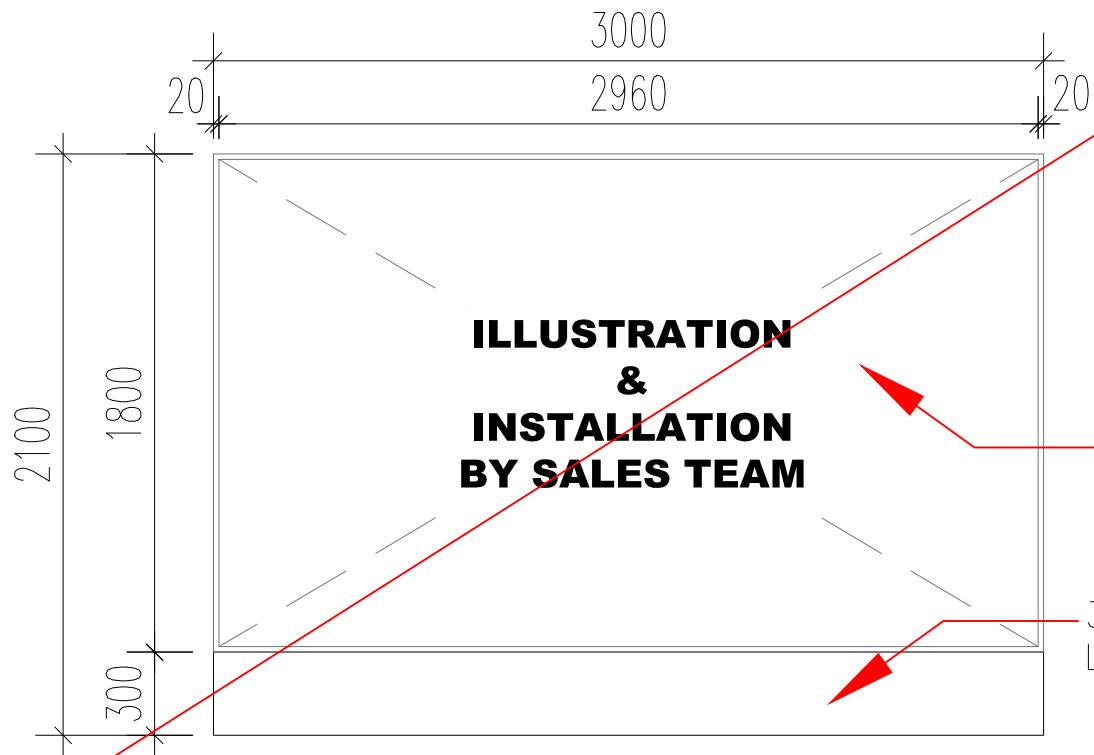

ADVERTISING BOARD  
FRONT ELEVATION

BLACK LAMINATE BACKING

LIGHTBOX PANEL WITH CONCEALED  
LED BACK LIGHT & BLACK LAMINATE  
FRAME


3000 x 300 BASE WITH BLACK  
LAMINATE



ADVERTISING BOARD  
REAR ELEVATION


|  |   |                                                                                               |         |          |                                                  |          |
|--|---|-----------------------------------------------------------------------------------------------|---------|----------|--------------------------------------------------|----------|
|  | THIS DRAWING IS COPYRIGHTED. CONTRACTORS MUST CHECK ALL DIMENSIONS ON SITE. ONLY FIGURED DIMENSIONS ARE TO BE WORKED FROM. DISCREPANCIES MUST BE REPORTED IMMEDIATELY TO ARCHITECT , S.O.,DESIGNER & CLIENT BEFORE PROCEEDING. | PROJECT<br>LOT 26662 – BUKIT BARU SALES GALLERY<br><br><b>MAIN LOBBY<br/>INTERIOR DETAILS</b> | SCALE   | AS SHOWN | DRAWING TITLE<br><b>ADVERTISING BOARD DETAIL</b> | REVISION |
|  |   |                                                                                               | DRAWN   | ALIAA    |                                                  |          |
|  |   |                                                                                               | CHECKED | AMIN     | DRAWING NO<br><b>09</b>                          | 01       |
|  |   |                                                                                               | DATE    | 31/07/26 |                                                  |          |

ALL LOOSE FURNITURE &  
MATERIAL CODE TO CLIENT  
SELECTION

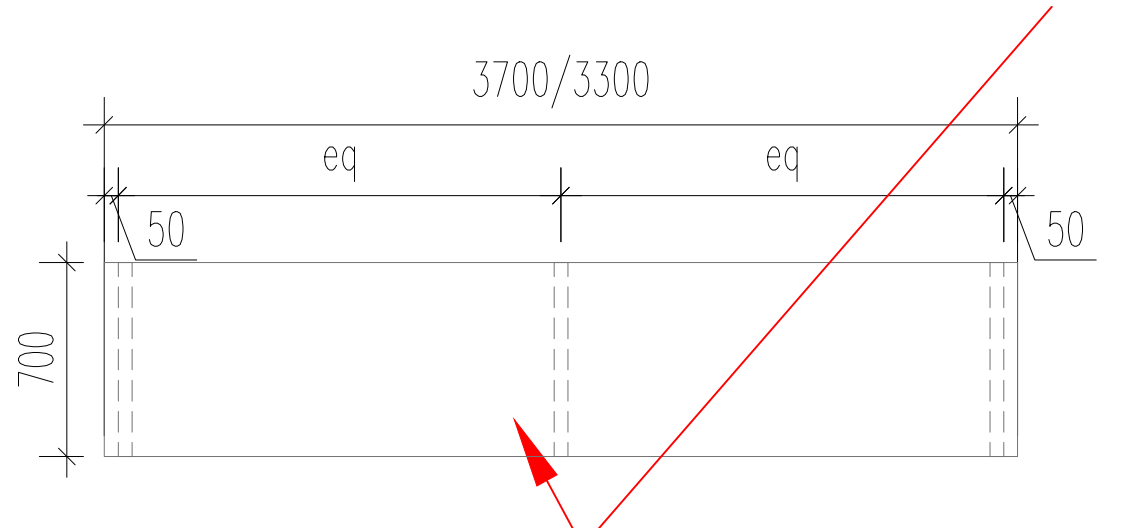


**BENCH - SEATING AREA 01 & 02**  
**PLAN**

BENCH WITH TIMBER FINISH

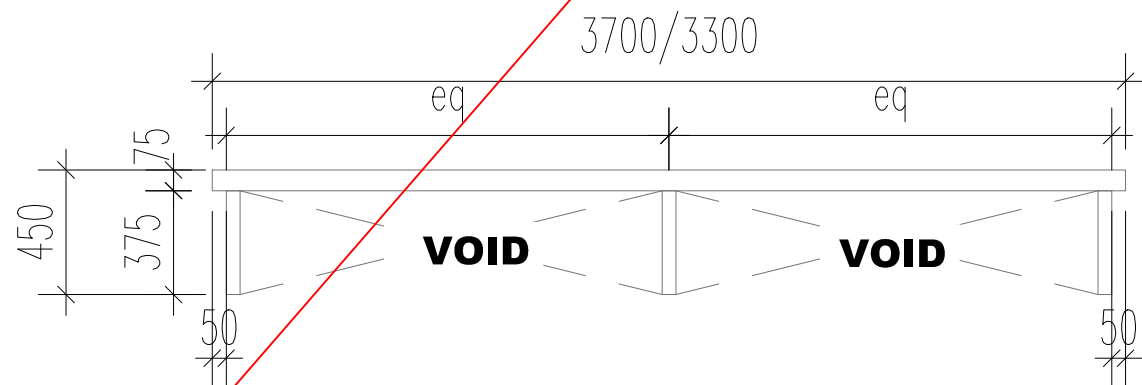


**BENCH - SEATING AREA 01& 02**  
**FRONT ELEVATION**

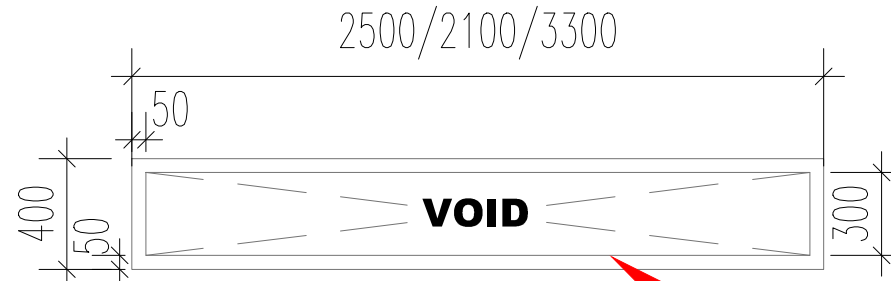


**PLANTER BOX SEATING AREA 01 & 02**  
**PLAN / TOP**


PLANTER BOX WITH TEXTURED FINISH

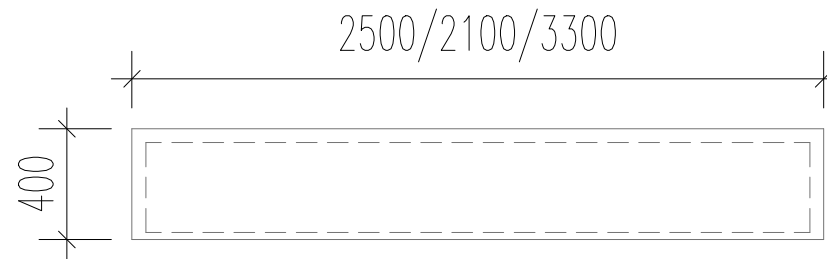


**PLANTER BOX - SEATING AREA 01& 02**  
**FRONT & REAR ELEVATION**


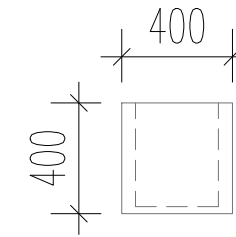


**PLANTER BOX**  
**SIDE ELEVATION**

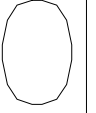
|  |   |                                                                                               |         |          |                                            |   |
|--|---|-----------------------------------------------------------------------------------------------|---------|----------|--------------------------------------------|---|
|  | THIS DRAWING IS COPYRIGHTED. CONTRACTORS MUST CHECK ALL DIMENSIONS ON SITE. ONLY FIGURED DIMENSIONS ARE TO BE WORKED FROM. DISCREPANCIES MUST BE REPORTED IMMEDIATELY TO ARCHITECT , S.O.,DESIGNER & CLIENT BEFORE PROCEEDING. | PROJECT<br>LOT 26662 – BUKIT BARU SALES GALLERY<br><br><b>MAIN LOBBY<br/>INTERIOR DETAILS</b> | SCALE   | AS SHOWN | DRAWING TITLE<br><b>PLANTER BOX DETAIL</b> | REVISION   |
|  |   |                                                                                               | DRAWN   | ALIAA    |                                            |   |
|  |   |                                                                                               | CHECKED | AMIN     | DRAWING NO<br><b>10</b>                    |   |
|  |   |                                                                                               | DATE    | 31/07/26 |                                            |   |

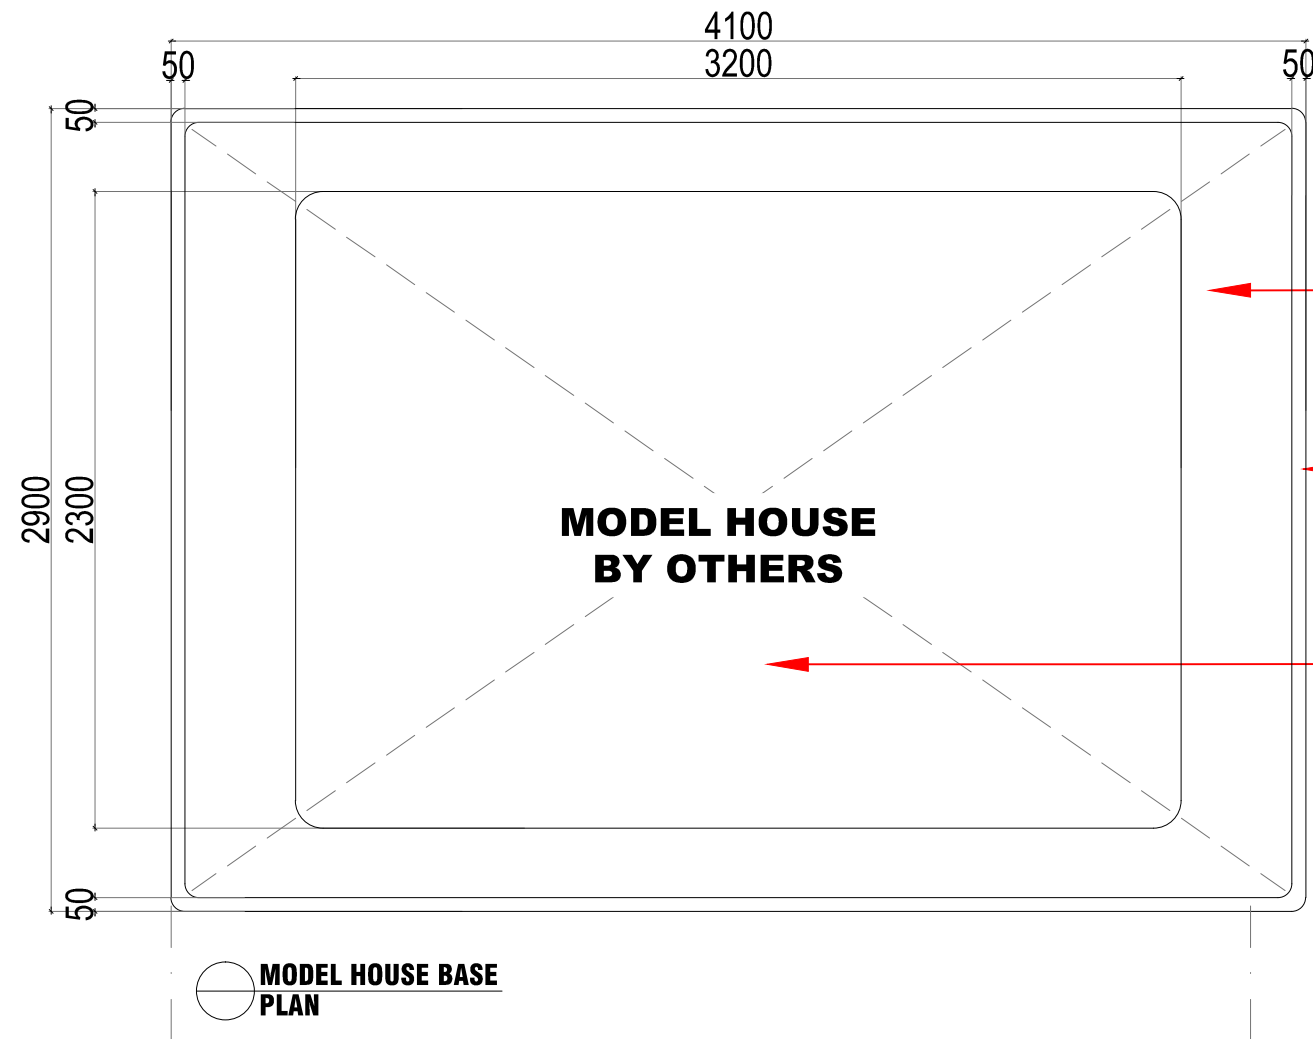


- MODEL HOUSE BASE STRUCTURE TO CARPENTER DETAILS
- 50mm(H) RIM BOARDER WITH LAMINATE FINISHES [CODE:TP7-53011G VOLAKAS-MARBLE FINISHES]
- TOP TO BE PAINT IN BLACK
- ACCESS FOR MAINTAINANCE

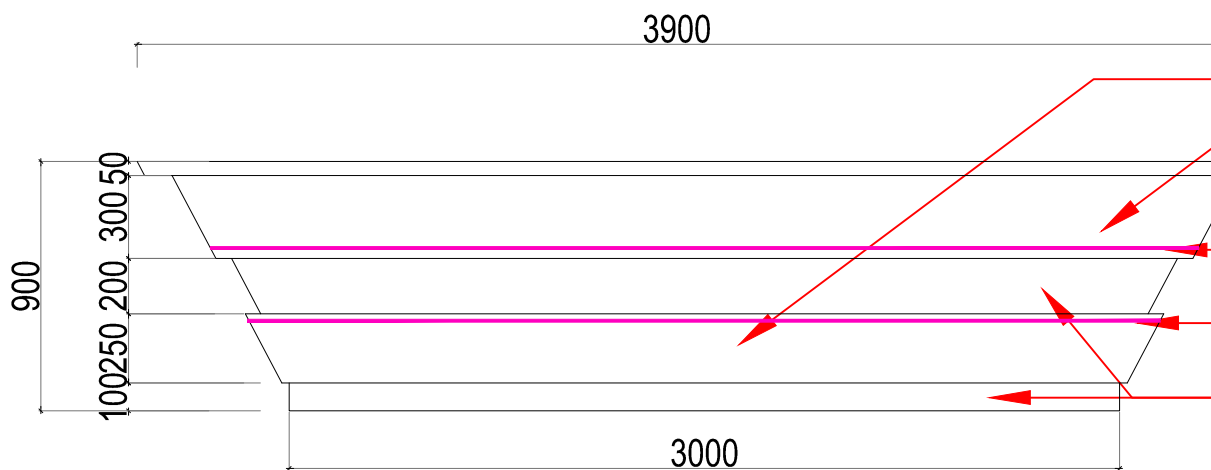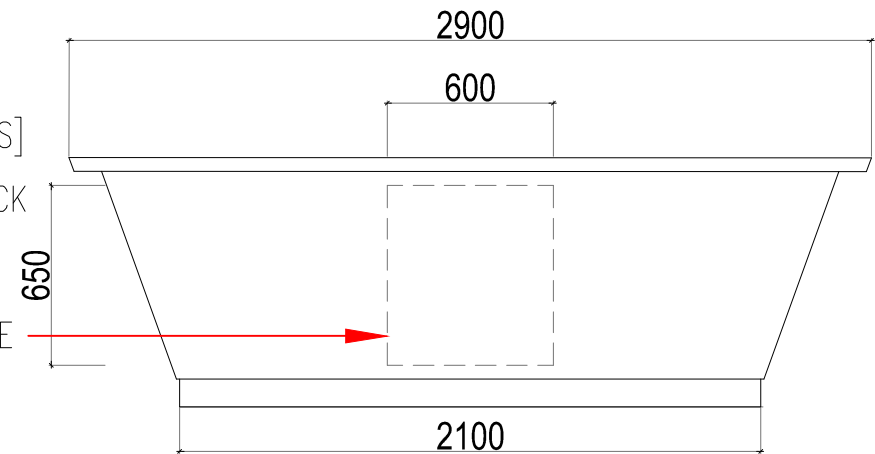


- LAMINATE FINISHES [CODE: CODE:TP7-53011G VOLAKAS-MARBLE FINISHES]
- LED LIGHT
- BLACK GLOSSY LAMINATE

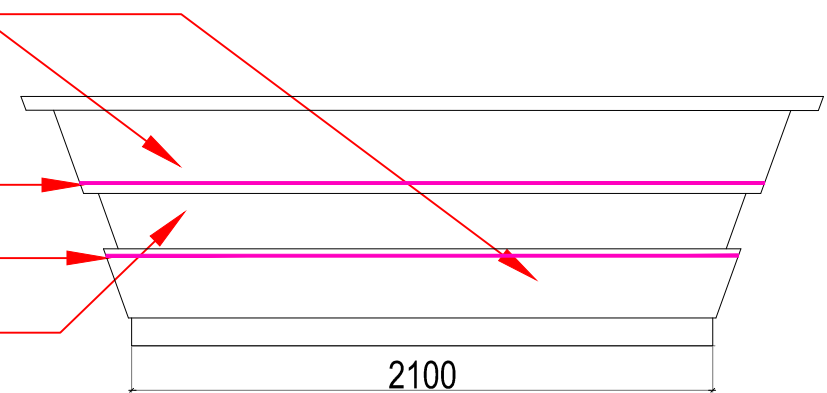

|  |   |                                                                                               |         |          |                                 |          |
|--|---|-----------------------------------------------------------------------------------------------|---------|----------|---------------------------------|----------|
|  | THIS DRAWING IS COPYRIGHTED. CONTRACTORS MUST CHECK ALL DIMENSIONS ON SITE. ONLY FIGURED DIMENSIONS ARE TO BE WORKED FROM. DISCREPANCIES MUST BE REPORTED IMMEDIATELY TO ARCHITECT , S.O.,DESIGNER & CLIENT BEFORE PROCEEDING. | PROJECT<br>LOT 26662 – BUKIT BARU SALES GALLERY<br><br><b>MAIN LOBBY<br/>INTERIOR DETAILS</b> | SCALE   | AS SHOWN | DRAWING TITLE                   | REVISION |
|  |   |                                                                                               | DRAWN   | ALIAA    | <b>MODEL HOUSE BASE DETAILS</b> |          |
|  |   |                                                                                               | CHECKED | AMIN     | DRAWING NO                      | 01       |
|  |   |                                                                                               | DATE    | 31/07/26 | <b>11</b>                       |          |

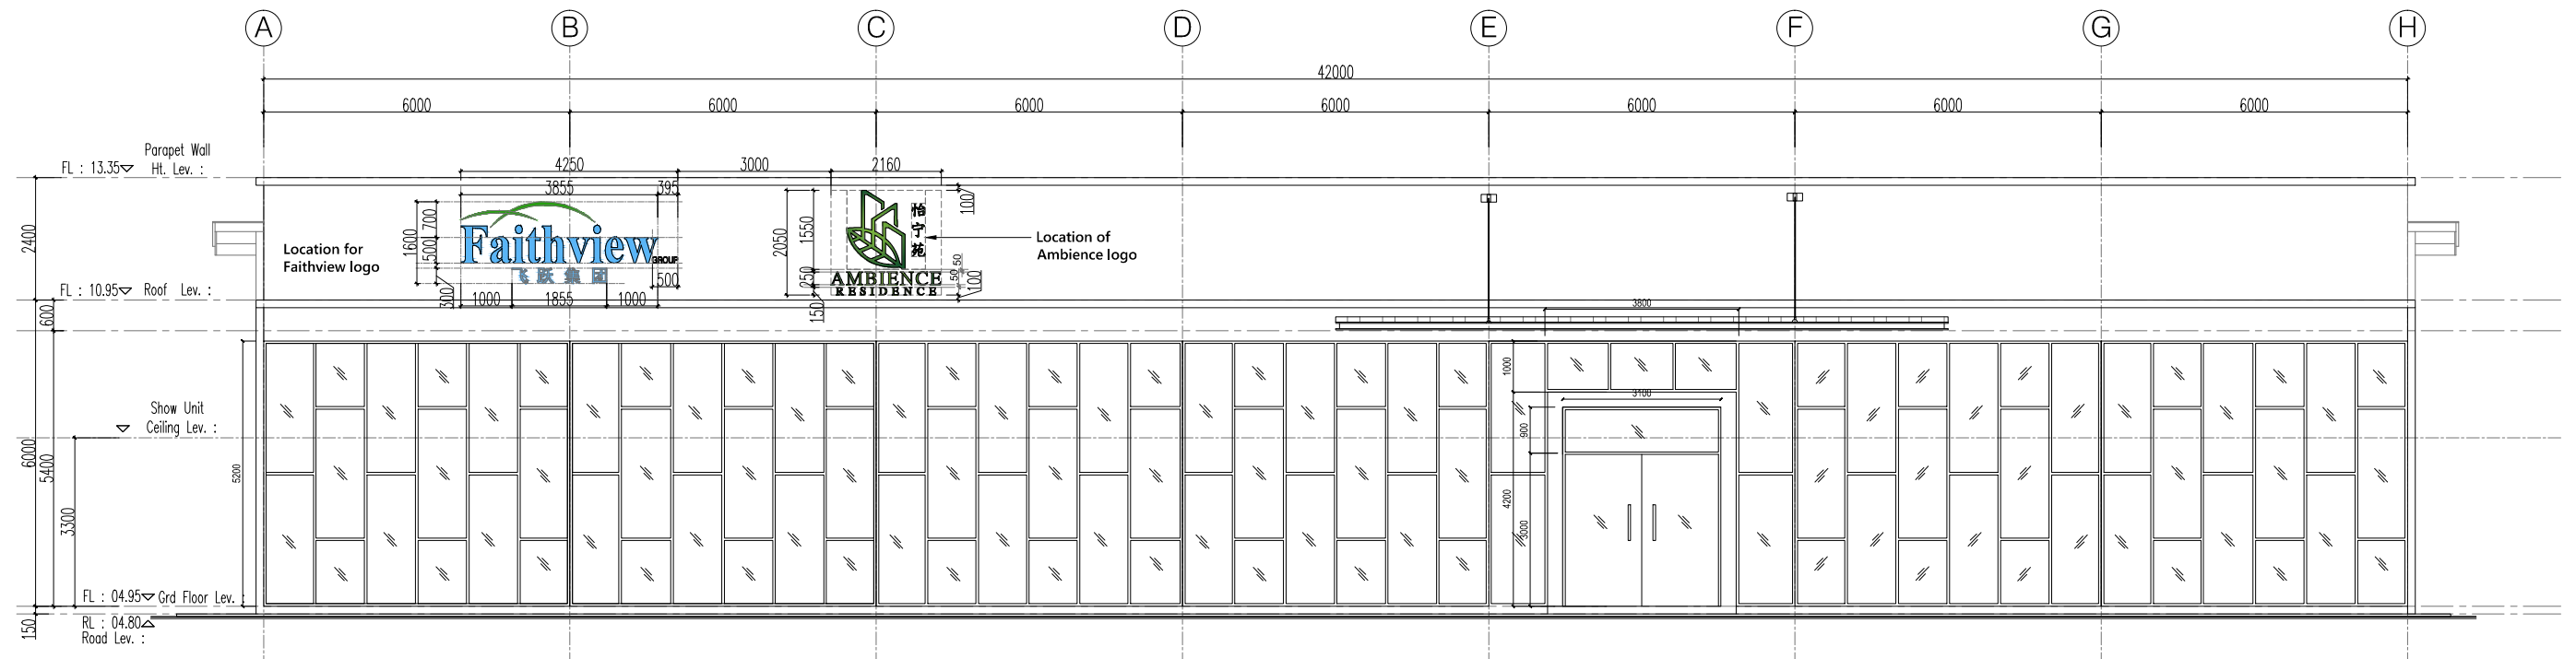


○ **AMBIENCE LOGO DETAIL  
FRONT ELEVATION**

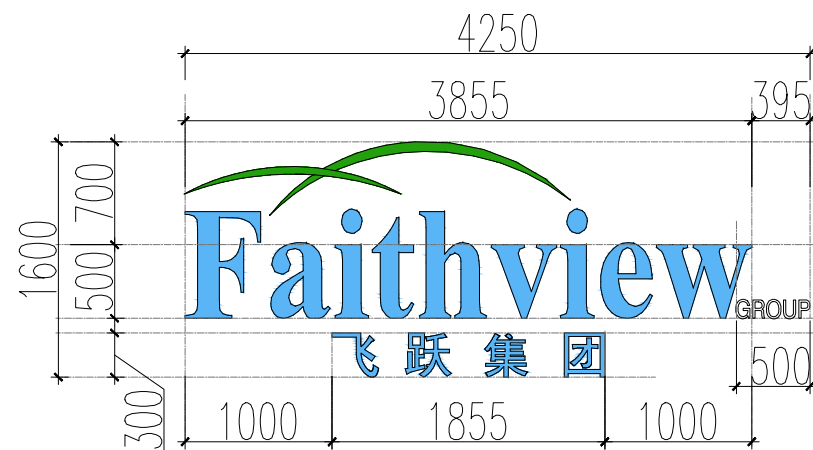

○ **FAITHVIEW LOGO DETAIL  
DETAILS ELEVATION**

COLOR CODE :

- CMYK : #62bb46
- CMYK : #00aeef
- WHITE

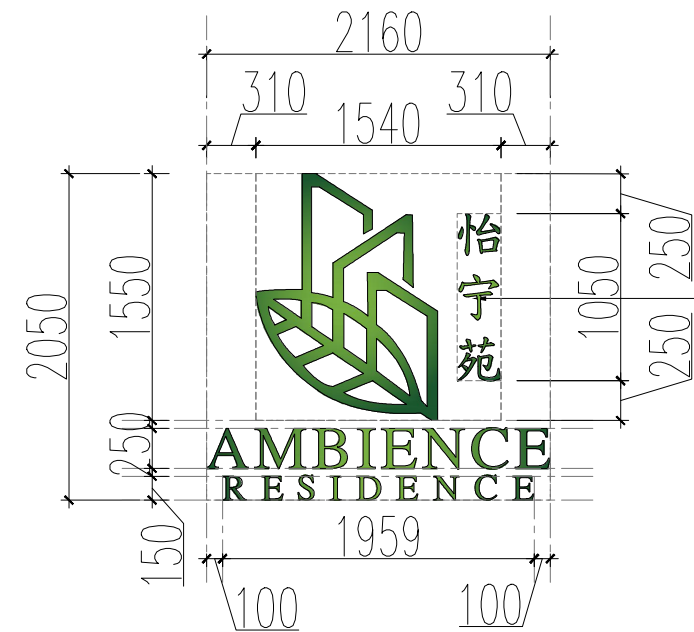

○ **AMBIENCE LOGO DETAIL  
DETAILS ELEVATION**

COLOUR TO FOLLOW AI  
REFERENCE

|  |   |                                                                                              |         |          |                                      |          |
|--|---|----------------------------------------------------------------------------------------------|---------|----------|--------------------------------------|----------|
|  | THIS DRAWING IS COPYRIGHTED. CONTRACTORS MUST CHECK ALL DIMENSIONS ON SITE. ONLY FIGURED DIMENSIONS ARE TO BE WORKED FROM. DISCREPANCIES MUST BE REPORTED IMMEDIATELY TO ARCHITECT , S.O., DESIGNER & CLIENT BEFORE PROCEEDING. | PROJECT<br>LOT 26662 – BUKIT BARU SALES GALLERY<br><br><b>SALES GALLERY EXTERIOR DETAILS</b> | SCALE   | AS SHOWN | DRAWING TITLE<br><b>LOGO DETAILS</b> | REVISION |
|  |   |                                                                                              | DRAWN   | ALIAA    |                                      |          |
|  |   |                                                                                              | CHECKED | AMIN     | DRAWING NO<br><b>01</b>              | ○ ○      |
|  |   |                                                                                              | DATE    | 10/07/26 |                                      |          |